1-maydon bosh rejasi: ekin maydoni, ferma va ilmiy markaz · 419,0 ga

M 1:5000. O‘lchamlar metrda

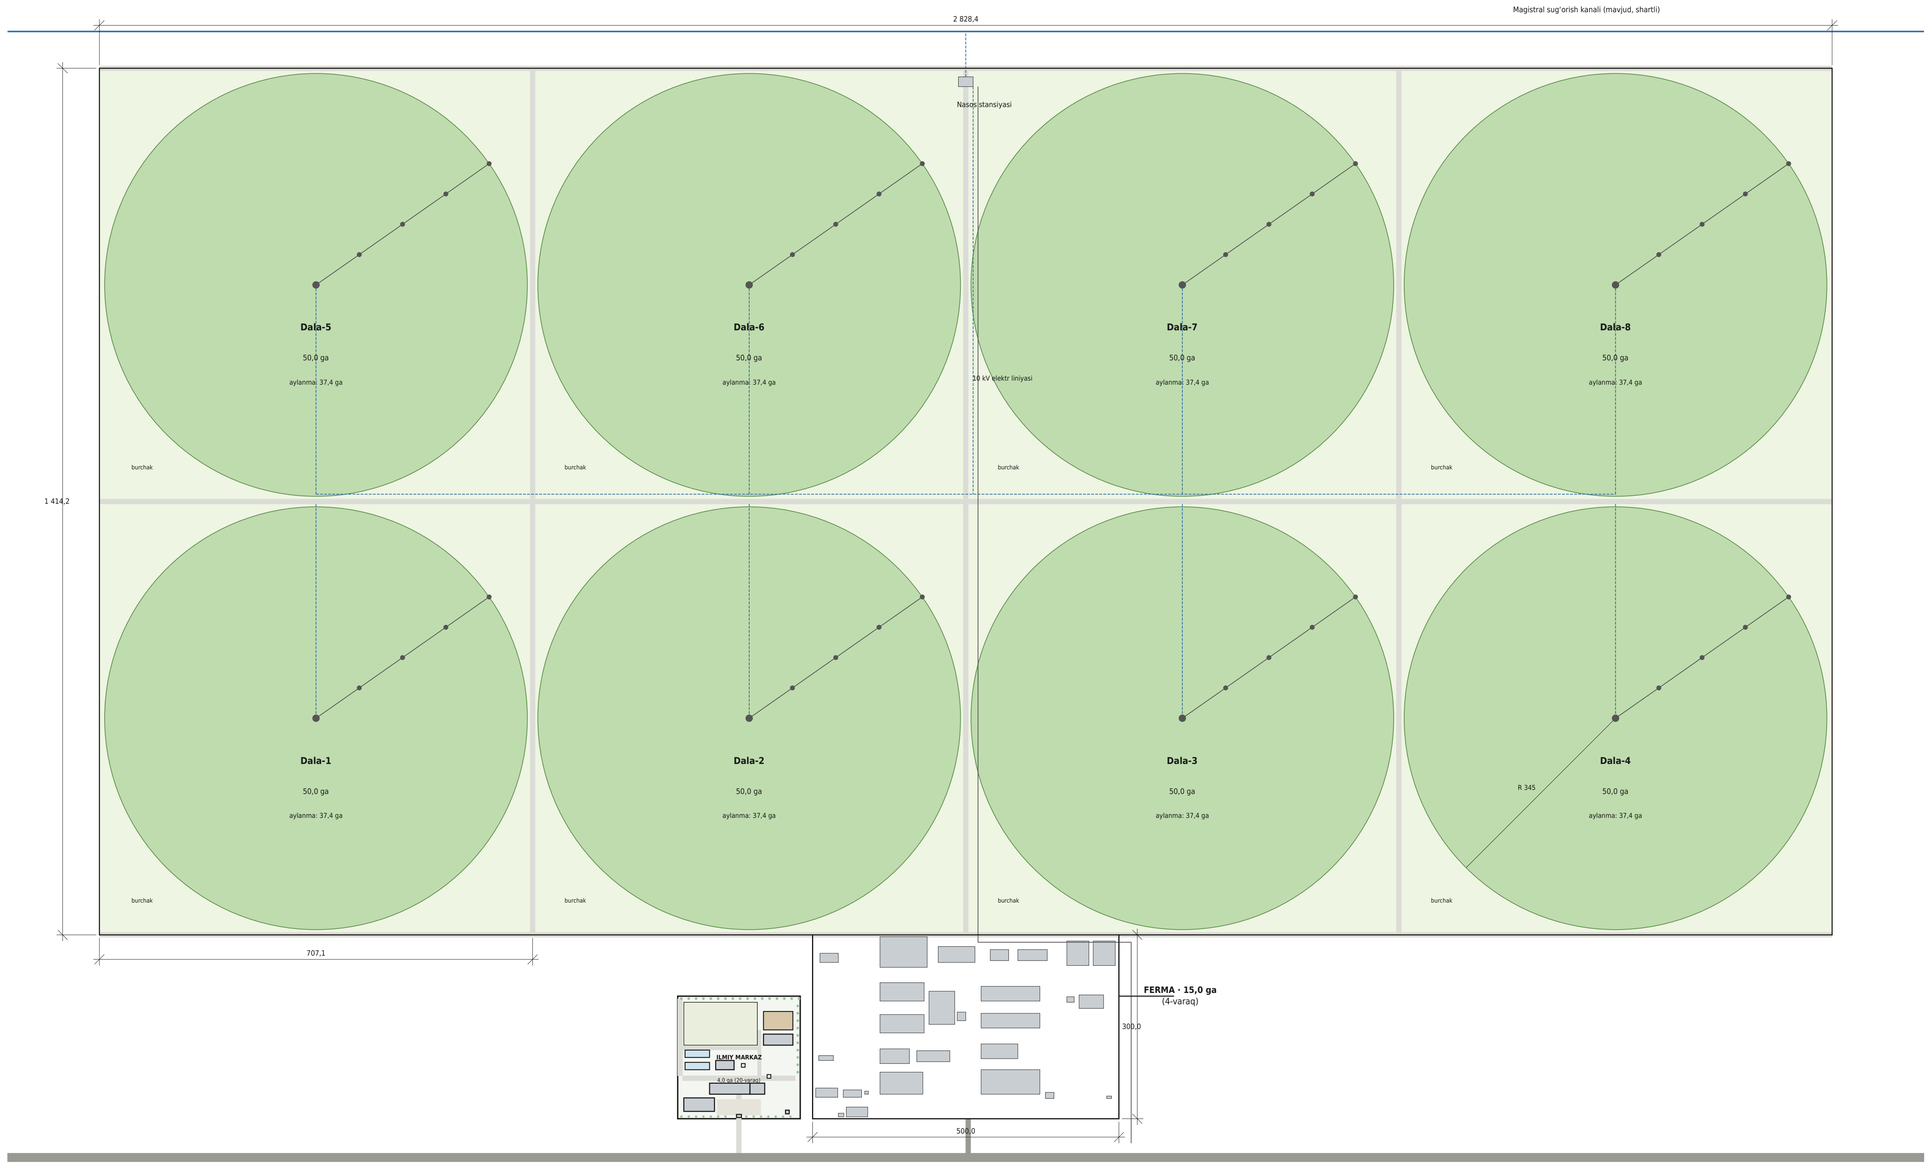

Ekinlar tuzilmasi

Ekin (o‘rtacha almashlab ekish)	Maydon, ga	Hosil
Beda (pichan, 4–5 o‘rim)	140	12 t/ga
Makkajo‘xori silos	100	45 t/ga
Kuzgi arpa (don + somon)	160	5 + 3 t/ga
Takroriy makkajo‘xori silos (arpadan keyin)	120	35 t/ga

Yer balansi

Maydon tarkibi	ga	%
Ekin maydoni (8 dala × 50,0 ga)	400,0	95,47
shu jumladan aylanma doiralar (8 × 37,4)	299,1	
burchaklar (egatlab sug‘oriladi)	95,2	
dala yo‘llari (8 m)	5,7	
Ferma (500 × 300 m)	15,0	3,58
Ilmiy-innovatsion markaz (200 × 200 m)	4,0	0,95
Jami 1-maydon	**419,0**	**100**

Eslatmalar

1. Har bir dalada bitta aylanma sug‘orish mashinasi (radiusi 345 m); 8 ta mashina nasos stansiyasidan bosimli quvur bilan ta’minlanadi.
2. Dala burchaklari beda va boshqa ko‘p yillik ekinlar uchun egatlab sug‘oriladi.
3. Ferma massivning janubiy chetida, o‘rtada; eng uzoq dala markazigacha ≈ 1,5 km (yo‘l bo‘yicha ≈ 2,1 km).
4. Ilmiy markaz fermaning old tomonida, avtomobil yo‘li bo‘yida, fermadan 20 m; o‘z kirish yo‘li bilan.
5. Kanal, yo‘l va elektr liniyasi shartli ko‘rsatilgan; massiv tanlangach aniqlanadi.

Almashtirilgan inv. №

Inobr va sana

Alb nusxa inv. №

O‘zg.	Varaq	Hujjat №	Imzo	Sana
Ishlab chiqdi				10.2026
Tekshirdi				10.2026
Bosh muhandis				10.2026
Normativ nazorat				10.2026
Tasdiqladi				10.2026

TMS-2026-TEO

Toshkent Meat Solutions — integratsiyalashgan go‘sht klasteri

1-maydon bosh rejasi: ekin maydoni, ferma va ilmiy markaz (419,0 ga)

Masshtab: 1:5000

Bosqich	Varaq	Varaqlar
TEO oldi	3	21

Toshkent Meat Solutions
Toshkent viloyati, 2026