
Ferma bosh rejasi · 15,0 ga (500 × 300 m)

M 1:1000. O'lchamlar metrda. Shimol tomonda dalalar, janubda avtomobil yo'li

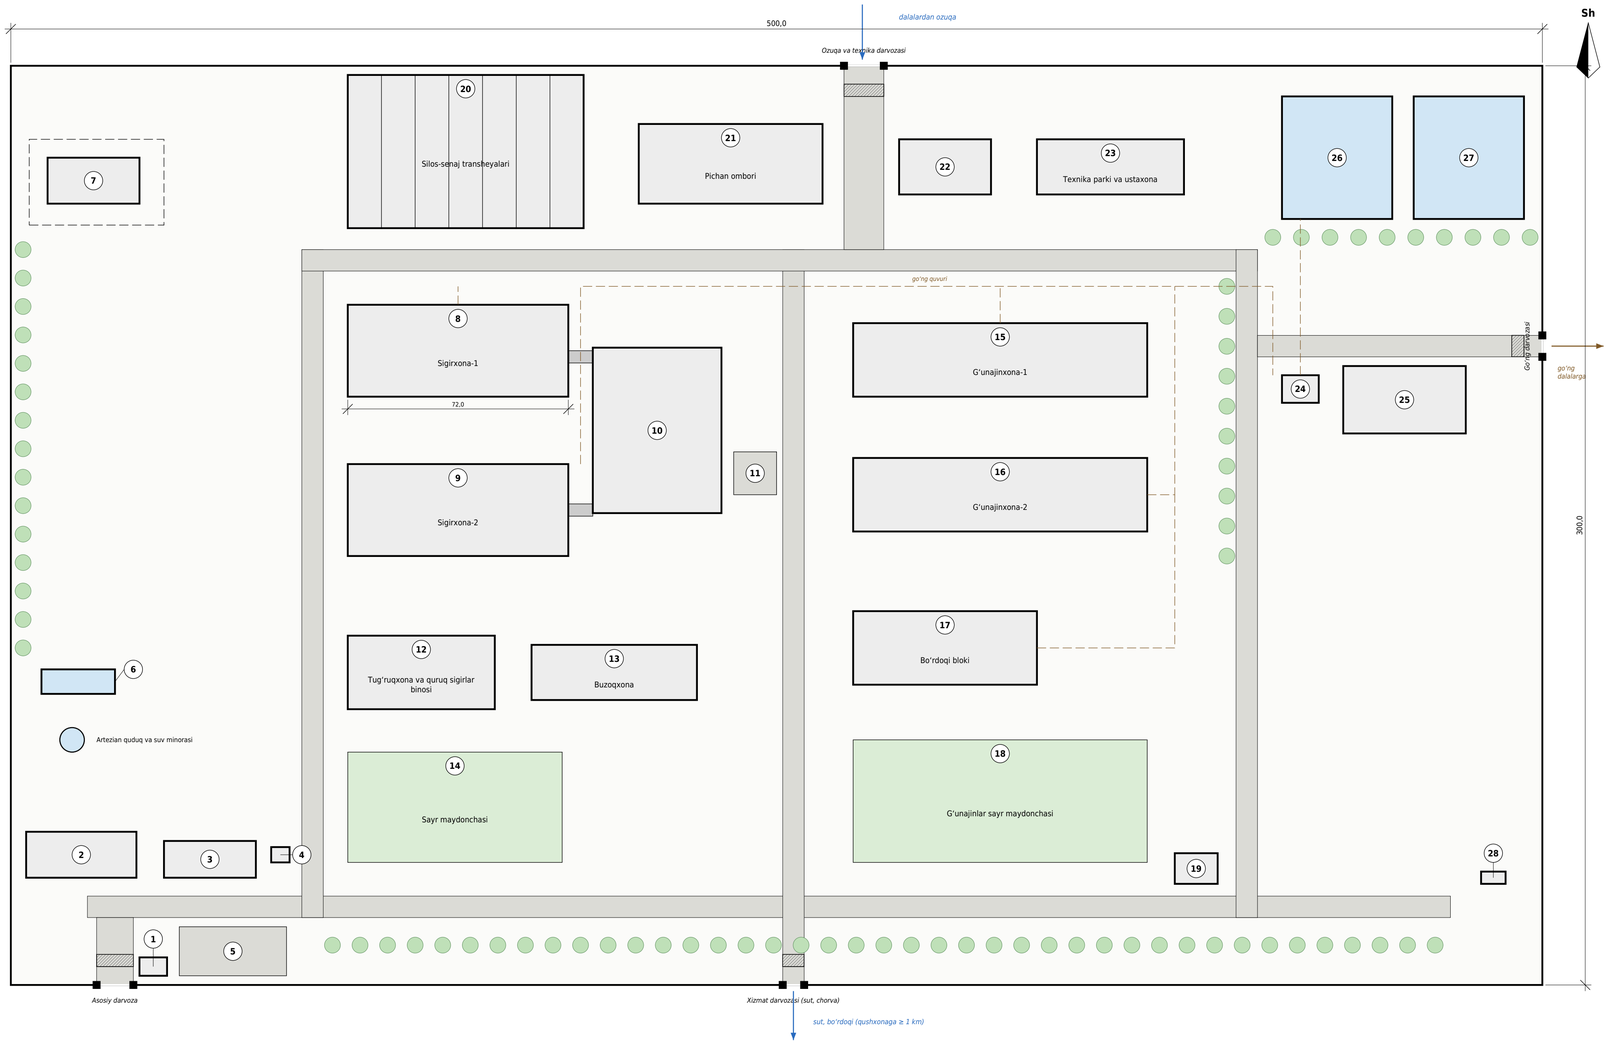

Binolar va inshootlar eksplikatsiyasi

№	Nomi	O'lchami, m	Maydoni, m²
1	Nazorat-o'tkazish punkti	9 × 6	54
2	Ma'muriy-maishiy bino (sanitariya o'tkazgichi bilan)	36 × 15	540
3	Veterinariya bloki va sun'iy urug'lantirish punkti	30 × 12	360
4	Transformator podstansiyasi 10/0,4 kV	6 × 5	30
5	Avtoturargoh (40 joy)	35 × 16	560
6	Yong'inga qarshi suv havzalari (2 × 100 m³)	24 × 8	192
7	Karantin va izolyator (alohida to'siq bilan)	30 × 15	450
8	Sigirxona-1 (200 boks, 180 sigir)	72 × 30	2 160
9	Sigirxona-2 (200 boks, 180 sigir)	72 × 30	2 160
10	Sog'ish zali (karusel, 40 joy) va sut bloki	42 × 54	2 268
11	Sut mashinasi maydonchasi	14 × 14	196
12	Tug'ruqxona va quruq sigirlar binosi (60 joy)	48 × 24	1 152
13	Buzoqxona (160 joy)	54 × 18	972
14	Sayr maydonchasi (quruq sigirlar)	70 × 36	2 520
15	G'unajinxona-1 (300 joy)	96 × 24	2 304
16	G'unajinxona-2 (300 joy)	96 × 24	2 304
17	Bo'rdoqi bloki (240 joy)	60 × 24	1 440
18	G'unajinlar sayr maydonchasi	96 × 40	3 840
19	Chorva yuklash rampasi va tarozi	14 × 10	140
20	Silos-senaj transheyalari (7 × 11 × 50 m)	77 × 50	3 850
21	Pichan ombori (shiypon)	60 × 26	1 560
22	Don ombori va kombikorm sexi	30 × 18	540
23	Texnika parki va ustaxona	48 × 18	864
24	Go'ng separatori binosi	12 × 9	108
25	Qattiq go'ng maydonchasi (beton, devorli)	40 × 22	880
26	Suyuq go'ng lagunasi-1 (≈ 5 000 m³)	36 × 40	1 440
27	Suyuq go'ng lagunasi-2 (≈ 5 000 m³)	36 × 40	1 440
28	O'lgan hayvonlarni vaqtincha saqlash (sovutgichli konteyner)	8 × 4	32

Shartli belgilar

- Binolar
- Yo'llar va maydonchalar (asfalt-beton)
- Sayr maydonchalari
- Suv havzasi, go'ng lagunasi
- Dezinfeksiya to'sig'i (dezbarer)
- Go'ng quvuri (yer ostida)
- Daraxtlar (sanitariya-himoya qatori)

Asosiy ko'rsatkichlar va eslatmalar

1. Uchastka maydoni 15,0 ga; binolar egallagan maydon ≈ 2,42 ga (qurilish zichligi ≈ 16%).
2. Toza oqim (ozuqa, sut) va iflos oqim (go'ng, o'lgan hayvonlar) alohida darvoza va yo'llar orqali yuradi; ular kesishmaydi.
3. Har bir darvozada isitiladigan dezinfeksiya to'sig'i; xodimlar faqat sanitariya o'tkazgichi orqali kiradi.
4. Karantin binosi alohida to'siq bilan o'ralgan, yangi keltirilgan hayvonlar 30 kun saqlanadi.
5. Go'ng lagunalari yopiq, 180 kunlik zaxira hajmiga mo'ljallangan; go'ng dalalarga o'g'it sifatida chiqariladi.
6. Qushxona bu uchastkada joylashmaydi: u 2-maydonda, fermadan kamida 1 000 m uzoqlikda.

Almashtirilgan inv. №

Imzo va sana

Asl nusxa inv. №

O'zg.	Varaq	Hujjat №	Imzo	Sana
Ishlab chiqdi				10.2026
Tekshirdi				10.2026
Bosh muhandis				10.2026
Normativ nazorat				10.2026
Tasdiqladi				10.2026

TMS-2026-TEO

Toshkent Meat Solutions — integratsiyalashgan go'sht klasteri

Ferma bosh rejasi (15,0 ga)

Masshtab: 1:1000

Bosqich	Varaq	Varaqlar
TEO oldi	4	21

Toshkent Meat Solutions Toshkent viloyati, 2026