

# Ferma: sog‘ish zali va ma’muriy bino fasadlari

Fermaning ko‘rgazmali binolari: yog‘och va antrasit, karusel ustida yorug‘lik fonari, tomda quyosh panellari


### Sog‘ish zali va sut bloki — sharqiy fasad · M 1:100

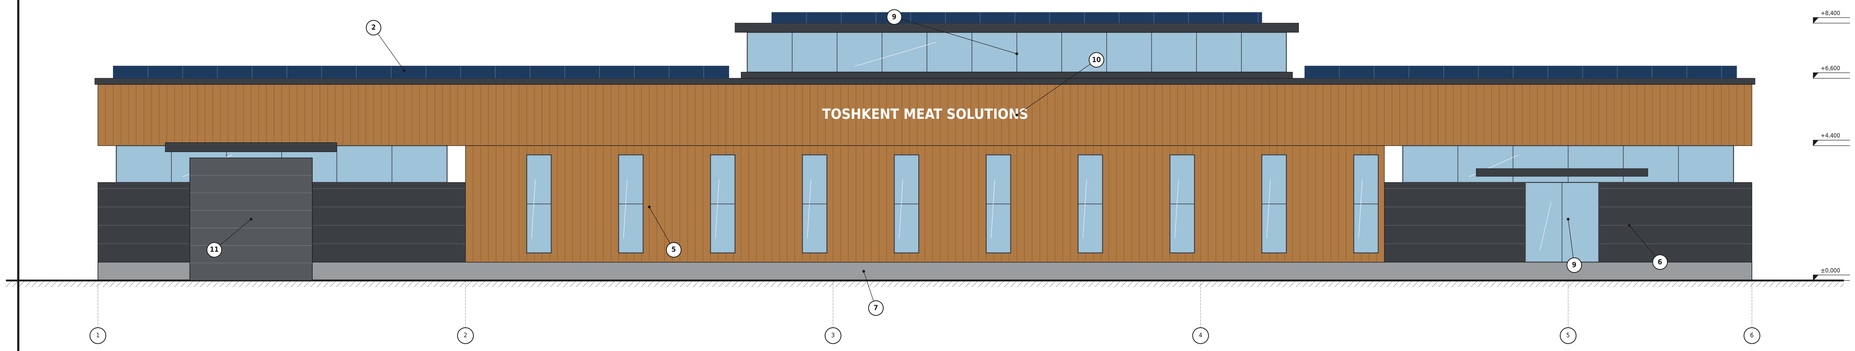


### Sog‘ish zali va sut bloki — janubiy fasad · M 1:100

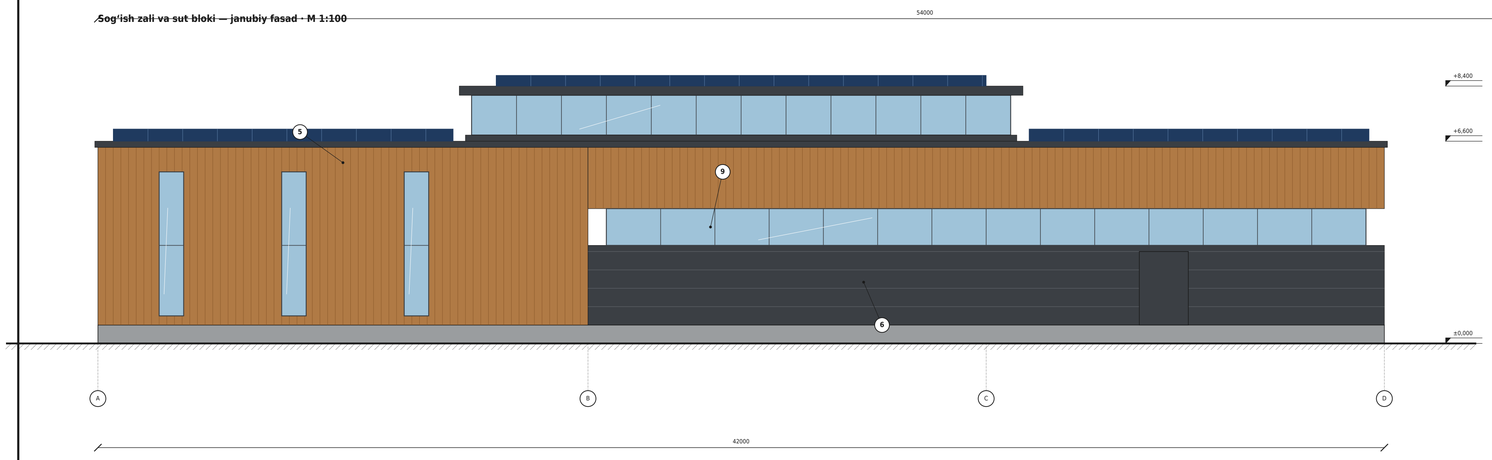


### Ma’muriy-maishiy bino (sanitariya o‘tkazgichi bilan) — janubiy fasad · M 1:100

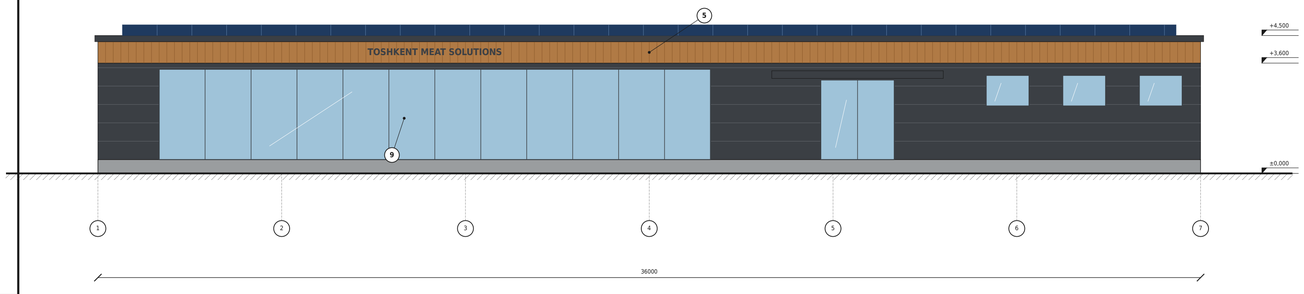


### Materiallar va ranglar

| | | |
|---|---|---|
| 2 | | Quyosh panellari: monokristall, qora ramkali |
| 5 | | Fasad lamellari: termoishlov berilgan qarag‘ay |
| 6 | | Metall fasad panellari, rama, eshiklar: antrasit, RAL 7016 |
| 7 | | Sokol: antrasit rangli beton |
| 9 | | Vitraj: alyuminiy profil, past emissiyali shisha |
| 10 | | Brend yozuvi: hajmli harflar, kechqurun yoritiladi |
| 11 | | Seksiyali darvoza va dok-shelter |

### Eslatmalar

1. Karusel ustidagi 18 × 18 m yorug‘lik fonari zalga tabiiy yorug‘lik beradi.
2. Tekis tomlarda quyosh panellari sharq-g‘arb 10° (14-varaq); parapet ustidan qisman ko‘rinadi.
3. Sharqiy fasadda sut mashinasi uchun darvoza (4 × 4 m) va mehmonlar kirishi.
4. Fasadlar 6-varaq rejasiga konseptual mos; 6-varaq bosh rejaga moslab qayta chizilgach, teshiklar joyi aniqlanadi.
5. Balandliklar konseptual, ishchi loyihada hisob bilan aniqlanadi.

| | | | | |
|---|---|---|---|---|
| O‘zg. | Varaq | Hujjat № | Imzo | Sana |
| Ishlab chiqdi | | | | 10.2026 |
| Tekshirdi | | | | 10.2026 |
| Bosh muhandis | | | | 10.2026 |
| Normativ nazorat | | | | 10.2026 |
| Tasdiqladi | | | | 10.2026 |

**TMS-2026-TEO**

Toshkent Meat Solutions — integratsiyalashgan go‘sht klasteri

**Sog‘ish zali va ma’muriy bino (ferma) fasadlari**

Masshtab: 1:100

| Bosqich | Varaq | Varaqlar |
|---|---|---|
| TEO oldi | 17 | 21 |

**Toshkent Meat Solutions**
**Toshkent viloyati, 2026**

Ahtapotning qarorno. №

Inspe ra soha

Ad ilacea ins. №