
1-maydon bosh rejasi: ekin maydoni va ferma · 415,0 ga

M 1:5000. O'lchamlar metrda

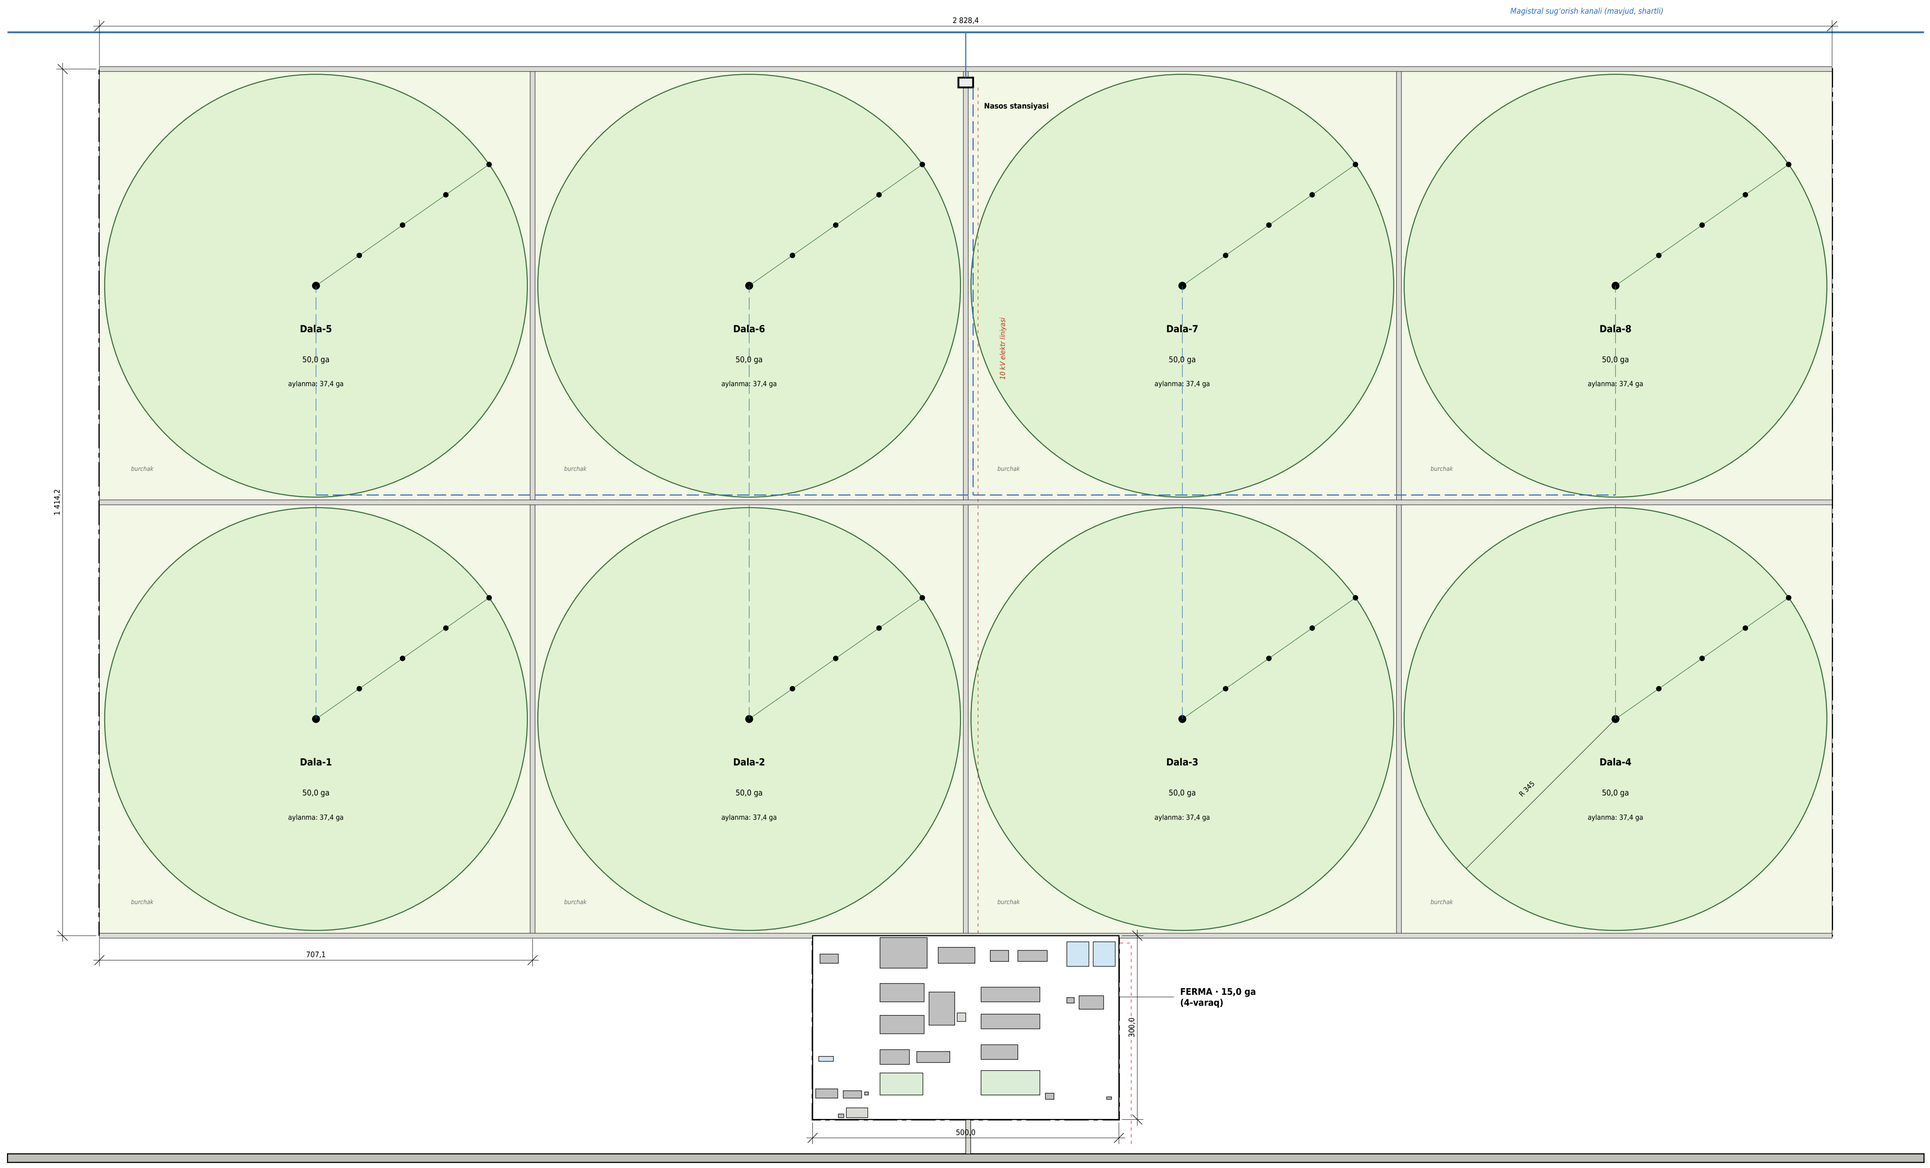

Ekinlar tuzilmasi

Ekin (o‘rtacha almashlab ekish)	Maydon, ga	Hosil
Beda (pichan, 4–5 o‘rim)	140	12 t/ga
Makkajo‘xori silos	100	45 t/ga
Kuzgi arpa (don + somon)	160	5 + 3 t/ga
Takroriy makkajo‘xori silos (arpadan keyin)	120	35 t/ga

Yer balansi

Maydon tarkibi	ga	%
Ekin maydoni (8 dala × 50,0 ga)	400,0	96,4
shu jumladan aylanma sug‘orish doiralari (8 × 37,4)	299,1	
burchaklar (egatlab sug‘oriladi)	95,2	
dala yo‘llari (8 m)	5,7	
Ferma (500 × 300 m)	15,0	3,6
Jami 1-maydon	415,0	100

Shartli belgilar

- Massiv chegarasi
- Aylanma sug‘orish doirasi (R 345 m)
- Dala burchaklari (egatlab sug‘orish)
- Dala yo‘llari
- Bosimli sug‘orish quvuri
- 10 kV elektr liniyasi

Eslatmalar

1. Har bir dalada bitta aylanma sug‘orish mashinasi (radiusi 345 m) o‘rnatiladi; 8 ta mashina nasos stansiyasidan bosimli quvur orqali ta’minlanadi.
2. Dala burchaklari beda va boshqa ko‘p yillik ekinlar uchun egatlab sug‘oriladi.
3. Ferma dalalar markaziga yaqin joylashgan: ozuqa va go‘ng tashish masofasi 2 km dan oshmaydi.
4. Kanal, yo‘l va elektr liniyasi shartli ko‘rsatilgan; massiv tanlangach aniqlanadi.

O'zg.	Varaq	Hujjat №	Imzo	Sana
Ishlab chiqdi				10.2026
Tekshirdi				10.2026
Bosh muhandis				10.2026
Normativ nazorat				10.2026
Tasdiqladi				10.2026

TMS-2026-TEO

Toshkent Meat Solutions — integratsiyalashgan go‘sht klasteri

1-maydon bosh rejasi: ekin maydoni va ferma (415,0 ga)

Masshtab: 1:5000

Bosqich	Varaq	Varaqlar
TEO oldi	3	19

Toshkent Meat Solutions
Toshkent viloyati, 2026

Almashtirilgan inv. №

Imzo va sana

Asl nusxa inv. №