
Sog‘ish zali (tashqi karusel, 40 joy) va sut bloki · 54 × 42 m

Reja M 1:100. O‘lchamlar millimetrda. Chizma bosh rejaga nisbatan 90° burilgan (4-varaq, 10-pozitsiya)

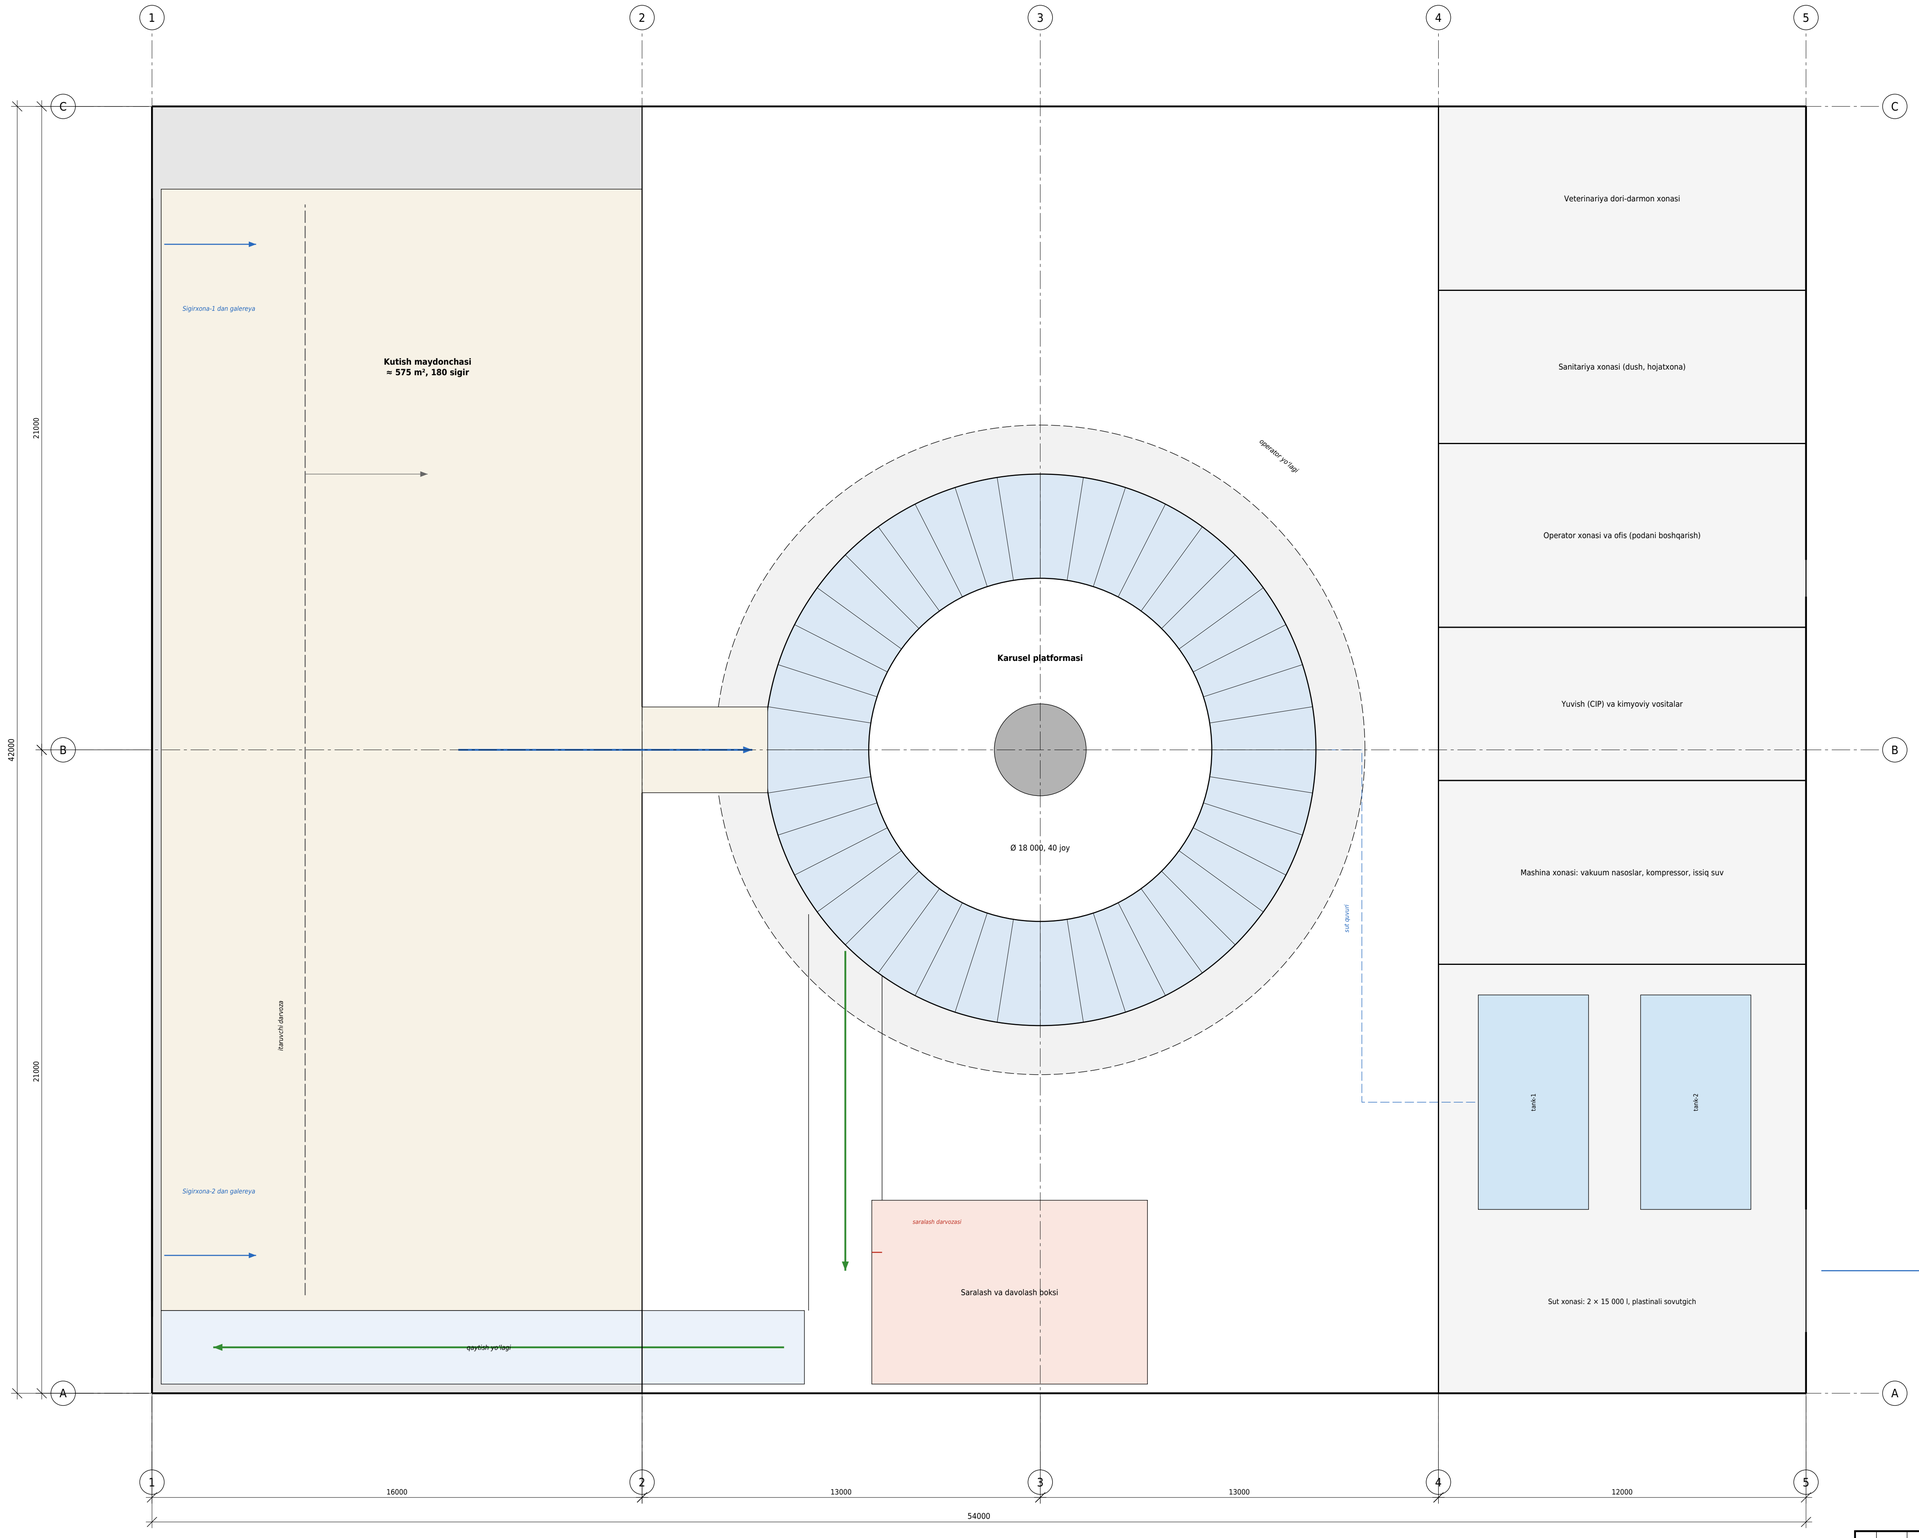

Asosiy ko‘rsatkichlar

Ko‘rsatkich	Qiymat
Karusel turi	tashqi, 40 joy
Platforma diametri	18 m
Bir aylanish	8–10 daqiqa
Unumdorlik	240–300 sigir/soat
Sog‘ish	kuniga 3 marta
Bir sog‘ish davomiyligi	≈ 1,5 soat (400 sigir)
Sut miqdori	≈ 7,3 t/sutka
Sut tanklari	2 × 15 000 l
Operatorlar	2–3 kishi/smena
Qurilish maydoni	2 268 m²

Eslatmalar

1. Sigirlar galereya orqali kutish maydonchasiga kiradi, itaruvchi darvoza ularni karuselga yaqinlashtiradi.
2. Sog‘ilgandan keyin sigir qaytish yo‘lagi orqali o‘z guruhiga qaytadi; davolash kerak bo‘lganlari saralash darvozasi orqali ajratiladi.
3. Sut yopiq quvur orqali to‘g‘ridan-to‘g‘ri sovutish tankiga tushadi va +4 °C gacha sovutiladi.
4. Har bir sigirning sut miqdori va holati identifikatsiya tizimi orqali qayd etiladi.

O‘zg.	Varaq	Hujjat №	Imzo	Sana
Ishlab chiqdi				10.2026
Tekshirdi				10.2026
Bosh muhandis				10.2026
Normanazorat				10.2026
Tasdiqladi				10.2026

TMS-2026-TEO

Toshkent Meat Solutions — integratsiyalashgan go‘sht klasteri

Sog‘ish zali (karusel, 40 joy) va sut bloki. Reja

Masshtab: 1:100

Bosqich	Varaq	Varaqlar
TEO oldi	6	19

Toshkent Meat Solutions
Toshkent viloyati, 2026

Almashtirilgan inv. №

Imzo va sana

Ad nusxa inv. №