
2-maydon bosh rejasi: qushxona, muzlatgich va qayta ishlash · 12,56 ga (400 × 314 m)

M 1:1000. O‘lchamlar metrda. 1-bosqich binolari; 2-bosqich uchun zaxira ko‘rsatilgan. Fermadan kamida 1 000 m uzoqlikda

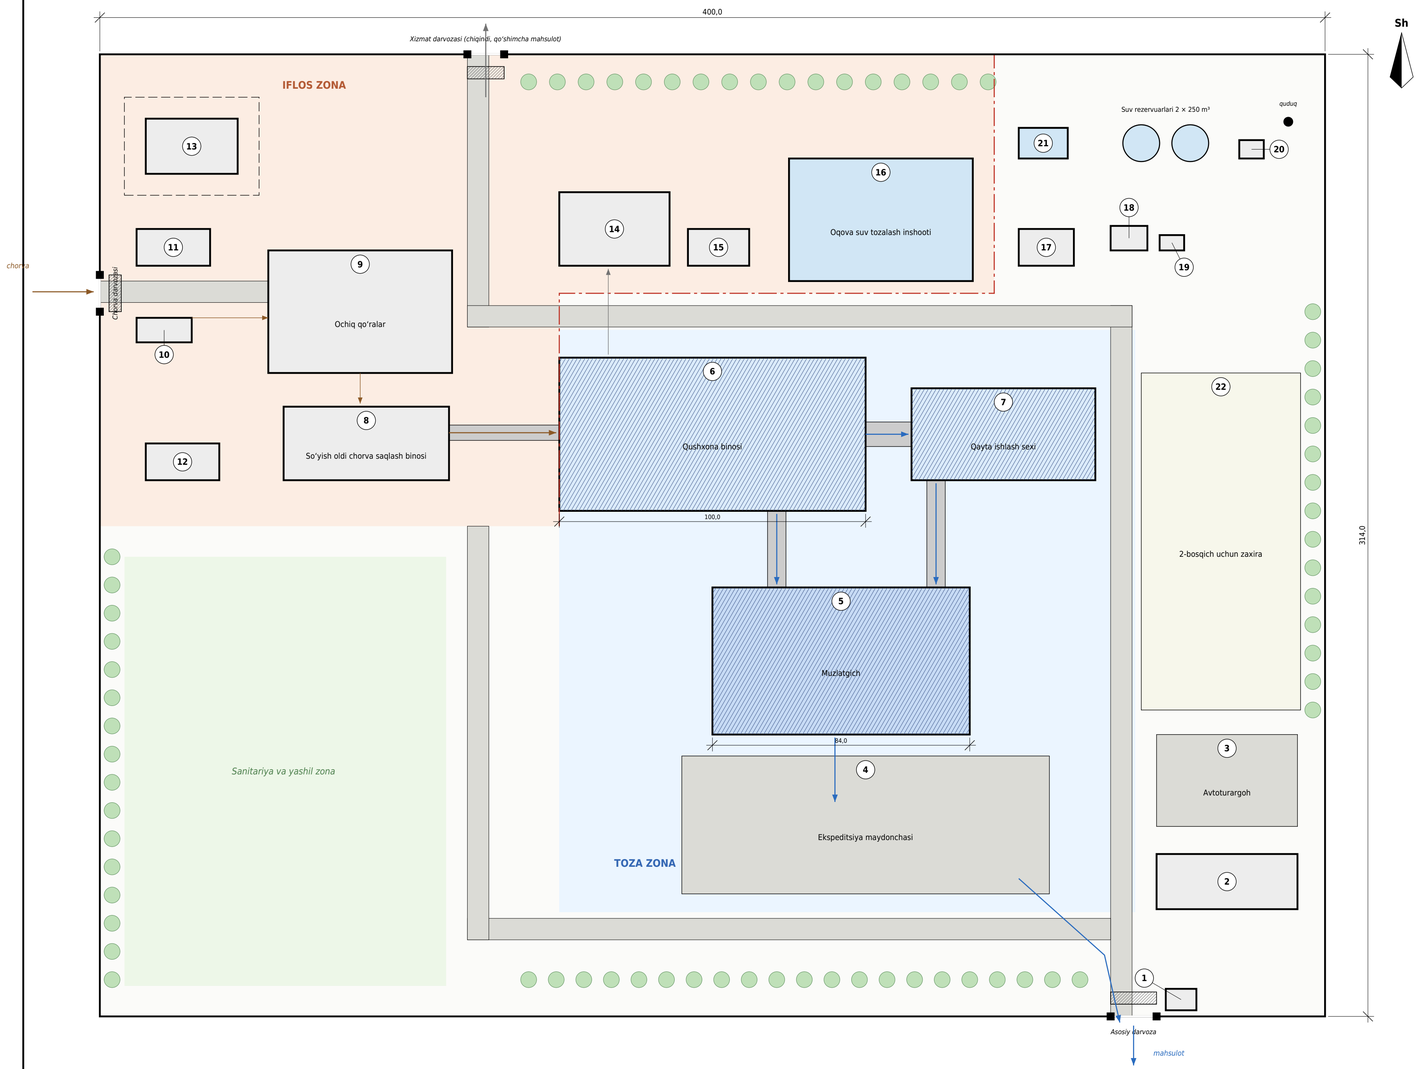

Binolar va inshootlar eksplikatsiyasi

№	Nomi	O‘lchami, m	Maydoni, m²
1	Nazorat-o‘tkazish punkti (asosiy)	10 × 7	70
2	Ma’muriy bino (2 qavat)	46 × 18	828
3	Avtoturargoh (60 joy)	46 × 30	1 380
4	Ekspeditsiya maydonchasi (yuk mashinalari)	120 × 45	5 400
5	Muzlatgich (3 000 t) va sovutish markazi	84 × 48	4 032
6	Qushxona binosi (so‘yish va tusha sovutish)	100 × 50	5 000
7	Qayta ishlash sexi	60 × 30	1 800
8	So‘yish oldi chorva saqlash binosi	54 × 24	1 296
9	Ochiq qo‘ralar (navesli)	60 × 40	2 400
10	Chorva tushirish rampasi va qabul joyi	18 × 8	144
11	Transport yuvish va dezinfeksiya punkti	24 × 12	288
12	Veterinariya laboratoriyasi va chorva qabul ofisi	24 × 12	288
13	Karantin, izolyator va sanitariya so‘yish xonasi	30 × 18	540
14	Qo‘shimcha mahsulot sexi (yog‘ eritish, suyak-go‘sht uni)	36 × 24	864
15	Teri va texnik chiqindilar ombori	20 × 12	240
16	Oqova suv tozalash inshooti (≈ 250 m³/sutka)	60 × 40	2 400
17	Bug‘ qozonxonasi	18 × 12	216
18	Bosh transformator podstansiyasi 10/0,4 kV	12 × 8	96
19	Rezerv dizel-generator	8 × 5	40
20	Nasos stansiyasi (suv ta’minoti)	8 × 6	48
21	Yong‘inga qarshi suv havzasi	16 × 10	160
22	2-bosqich uchun zaxira (muzlatgich kengaytmasi, kolbasa sexi)	52 × 110	5 720

Shartli belgilar

- Iflos zona: chorva qabuli, karantin, chiqindilar
- Toza zona: mahsulot, omborlar, ekspeditsiya
- Sovutiladigan ishlab chiqarish binolari
- Muzlatgich
- Tomdagi quyosh panellari (≈ 1,3 MW, faqat tomlarda)
- 2-bosqich uchun zaxira maydoni
- Yopiq galereyalar va chorva haydash yo‘lagi
- Chorva oqimi
- Mahsulot oqimi
- Iflos va toza zonalar chegarasi

Eslatmalar

1. Uchastka maydoni 12,56 ga; binolar egallagan maydon ≈ 1,82 ga (qurilish zichligi ≈ 14%).
2. Iflos oqim (chorva, chiqindilar) va toza oqim (go‘sht, mahsulot) alohida darvozalar orqali yuradi va kesishmaydi. Qushxona, muzlatgich va qayta ishlash sexi yopiq galereyalar bilan bog‘langan.
3. Quyosh panellari faqat qushxona, muzlatgich va qayta ishlash sexi tomlarida, balastli tizimda, tomni teshmasdan o‘rnatiladi.
4. Shamol yo‘nalishi aniqlangach iflos zona va oqova suv tozalash inshooti shamol bo‘yicha pastda bo‘ladigan qilib joylashtiriladi.
5. 2-bosqichda zaxira maydonida muzlatgich kengaytmasi va kolbasa sexi quriladi; ikkinchi smena uchun yangi bino talab qilinmaydi.

O‘zg.	Varaq	Hujjat №	Imzo	Sana
Ishlab chiqdi				10.2026
Tekshirdi				10.2026
Bosh muhandis				10.2026
Normativ nazorat				10.2026
Tasdiqladi				10.2026

TMS-2026-TEO

Toshkent Meat Solutions — integratsiyalashgan go‘sht klasteri

2-maydon bosh rejasi: qushxona va muzlatgich (12,56 ga)

Masshtab: 1:1000

Bosqich	Varaq	Varaqlar
TEO oldi	8	19

Toshkent Meat Solutions Toshkent viloyati, 2026

Almashtirilgan inv. №

Imzo va sana

Asl nusxa inv. №