
Qushxona binosi: so‘yish, ishlov berish va tusha sovutish · 100 × 50 m

Reja M 1:200. O‘lchamlar millimetrda. Quvvat: smenada 100 bosh qoramol (12,5 bosh/soat) va 300 bosh qo‘y-echki (37,5 bosh/soat)

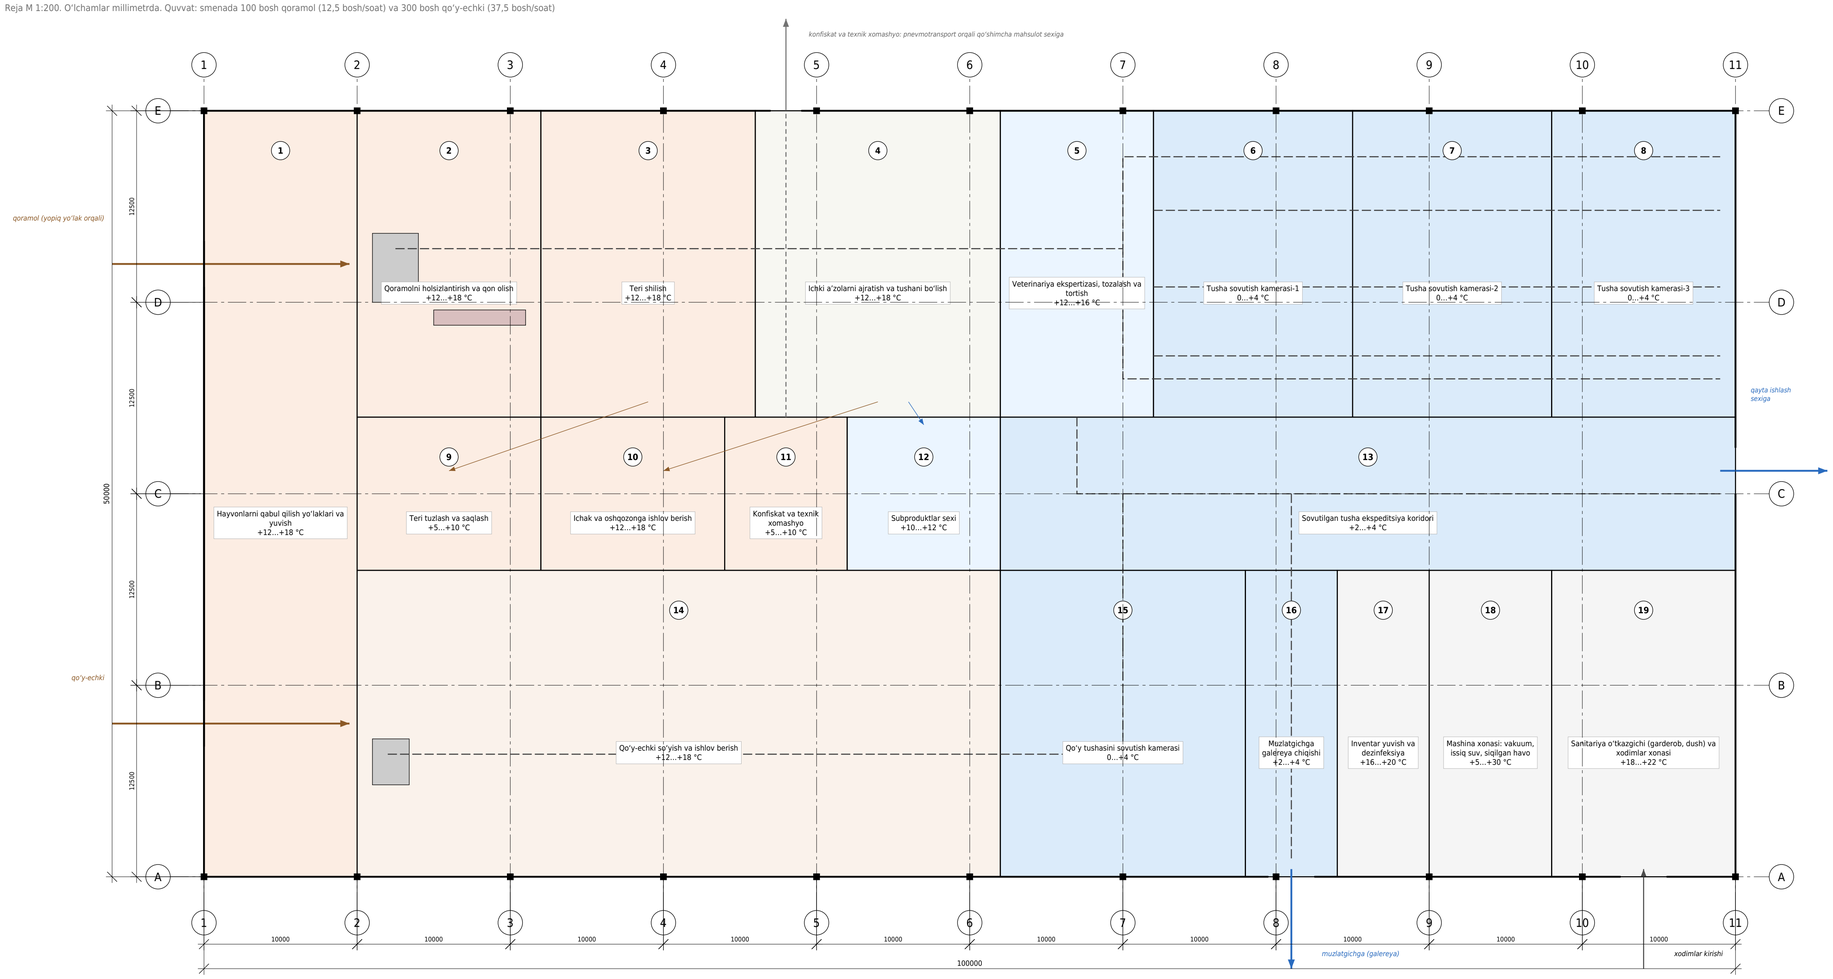

Xonalar eksplikatsiyasi

№	Xona nomi	Maydon, m²	Harorat, °C
1	Hayvonlarni qabul qilish yo‘laklari va yuvish	500	+12…+18
2	Qoramolni holsizlantirish va qon olish	240	+12…+18
3	Teri shilish	280	+12…+18
4	Ichki a’zolarni ajratish va tushani bo‘lish	320	+12…+18
5	Veterinariya ekspertizasi, tozalash va tortish	200	+12…+16
6	Tusha sovutish kamerasi-1	260	0…+4
7	Tusha sovutish kamerasi-2	260	0…+4
8	Tusha sovutish kamerasi-3	240	0…+4
9	Teri tuzlash va saqlash	120	+5…+10
10	Ichak va oshqozonga ishlov berish	120	+12…+18
11	Konfiskat va texnik xomashyo	80	+5…+10
12	Subproduktlar sexi	100	+10…+12
13	Sovutilgan tusha ekspeditsiya koridori	480	+2…+4
14	Qo‘y-echki so‘yish va ishlov berish	840	+12…+18
15	Qo‘y tushasini sovutish kamerasi	320	0…+4
16	Muzlatgichga galereya chiqishi	120	+2…+4
17	Inventar yuvish va dezinfeksiya	120	+16…+20
18	Mashina xonasi: vakuum, issiq suv, siqilgan havo	160	+5…+30
19	Sanitariya o‘tkazgichi (garderob, dush) va xodimlar xonasi	240	+18…+22

Texnologik ko‘rsatkichlar

Liniya	Quvvat
Qoramol	12,5 bosh/soat · 100 bosh/smena
Qo‘y-echki	37,5 bosh/soat · 300 bosh/smena
Tusha sovutish	3 kamera, ≈ 300 yarim tusha
Ish rejimi	1 smena, 300 kun/yil
2-smena	bino va liniyalar yetadi

Shartli belgilar

- Iflos zona xonalari
- Toza zona xonalari
- Sovutiladigan xonalar
- Osma yo‘l (tusha harakati)
- Hayvonlar va iflos xomashyo oqimi
- Toza mahsulot oqimi

Eslatmalar

1. Hayvonlar g‘arbdan, so‘yish oldi saqlash binosidan yopiq yo‘lak orqali kiradi; mahsulot sharq va janub tomondan galereyalar orqali chiqadi. Iflos va toza oqim kesishmaydi.
2. Har bir ishlov nuqtasida tusha va ichki a’zolar raqam bilan bog‘lanadi; veterinariya ekspertizasi 5-xonada yakunlanadi.
3. Halol talablari: so‘yish qiblaga qaratilgan, malakali so‘yuvchi tomonidan bajariladi.
4. Pollar nishabli, kislotaga chidamli plitka; devorlar shiftgacha yuviladigan qoplamali. Iflos va toza zonalar xodimlari alohida kiyim xonalaridan foydalanadi.
5. Tomda quyosh panellari (8-varaq); tomni kuchaytirish konstruktiv hisob bilan aniqlanadi.

O‘zg.	Varaq	Hujjat №	Imzo	Sana
Ishlab chiqdi				10.2026
Tekshirdi				10.2026
Bosh muhandis				10.2026
Normanazorat				10.2026
Tasdiqladi				10.2026

TMS-2026-TEO

Toshkent Meat Solutions — integratsiyalashgan go‘sht klasteri

Qushxona binosi. Reja va texnologik oqim

Masshtab: 1:200

Bosqich	Varaq	Varaqlar
TEO oldi	9	19

Toshkent Meat Solutions Toshkent viloyati, 2026

Almashtirilgan inv. №

Imzo va sana

Ad nuska inv. №