
Qayta ishlash sexi · 60 × 30 m

Reja M 1:100. O‘lchamlar millimetrda. Mahsulot: bo‘laklangan va vakuum qadoqlangan go‘sht, qiyma, yarim tayyor mahsulot

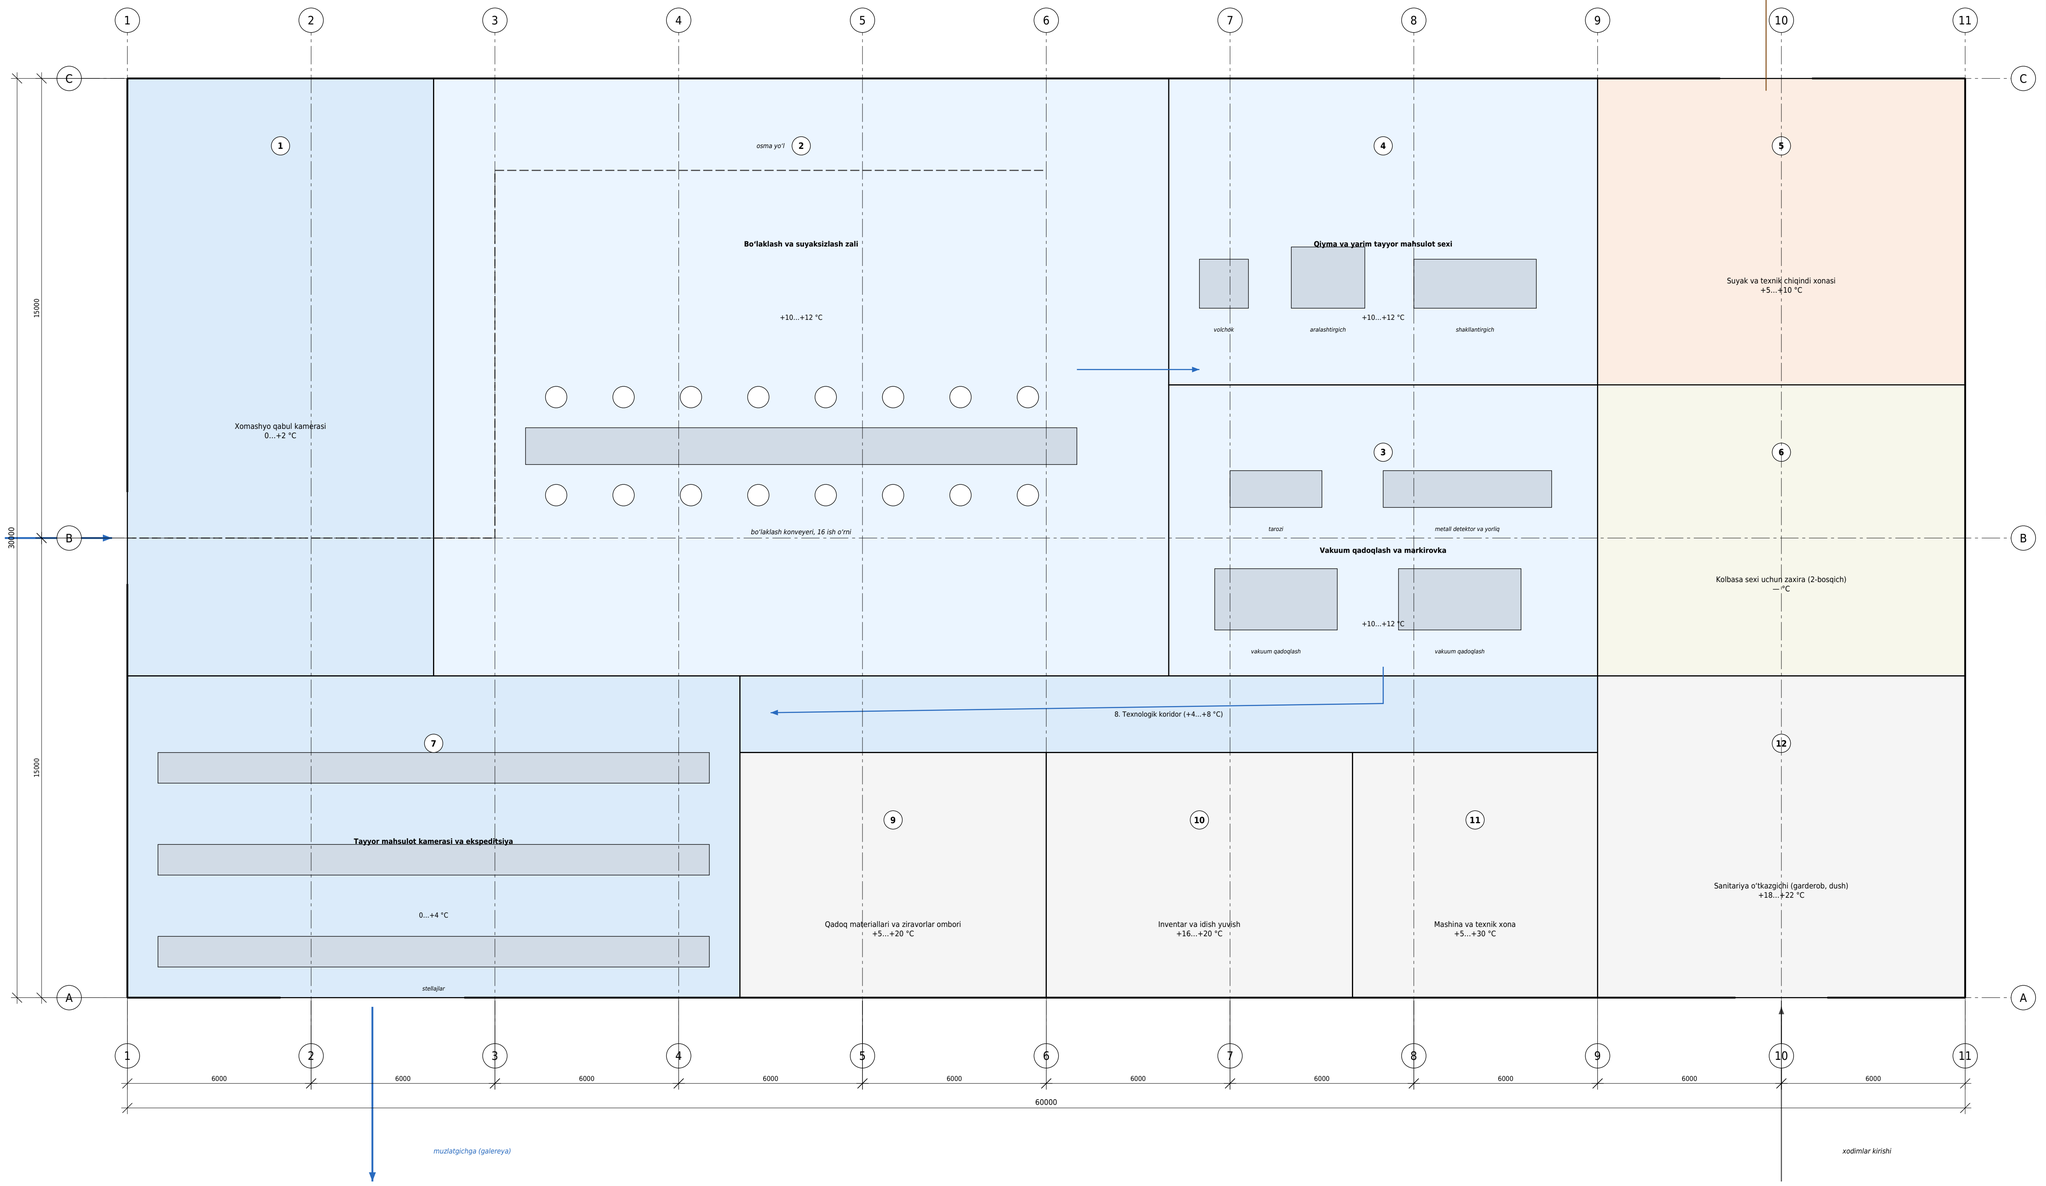

Xonalar

№	Xona	Maydon, m²	°C
1	Xomashyo qabul kamerasi	195	0…+2
2	Bo‘laklash va suyaksizlash zali	468	+10…+12
3	Vakuum qadoqlash va markirovka	133	+10…+12
4	Qiyma va yarim tayyor mahsulot sexi	140	+10…+12
5	Suyak va texnik chiqindi xonasi	120	+5…+10
6	Kolbasa sexi uchun zaxira (2-bosqich)	114	—
7	Tayyor mahsulot kamerasi va ekspeditsiya	210	0…+4
8	Texnologik koridor	70	+4…+8
9	Qadoq materiallari va ziravorlar ombori	80	+5…+20
10	Inventar va idish yuvish	80	+16…+20
11	Mashina va texnik xona	64	+5…+30
12	Sanitariya o‘tkazgichi (garderob, dush)	126	+18…+22

Asosiy jihozlar

Jihoz	Soni
Bo‘laklash konveyeri (16 ish o‘rni)	1
Vakuum qadoqlash mashinasi	2
Metall detektor, tarozi, yorliq printeri	1 liniya
Go‘sht maydalagich (volchok)	1
Qiyma aralashtirgich	1
Kotlet va yarim tayyor shakllantirgich	1
Osma yo‘l	≈ 50 m

Eslatmalar

1. Sovutilgan tusha qushxonadan galereya orqali osma yo‘lda keladi; tayyor mahsulot janubdagi galereya orqali muzlatgichning tayyor mahsulot kamerasiga o‘tadi.
2. Barqaror yilda ishlab chiqarilgan go‘shtning ≈ 35% i shu sexda qayta ishlanadi: 20% vakuum qadoqlangan bo‘laklar, 15% qiyma va yarim tayyor mahsulot.
3. Ishlab chiqarish zallarida harorat +10…+12 °C, havo filtrlanadi; pollar nishabli, trap bilan.
4. 6-xona 2-bosqichda kolbasa va pishirilgan mahsulotlar sexi uchun ajratilgan.

O‘zg.	Varaq	Hujjat №	Imzo	Sana
Ishlab chiqdi				10.2026
Tekshirdi				10.2026
Bosh muhandis				10.2026
Normativ nazorat				10.2026
Tasdiqladi				10.2026

TMS-2026-TEO

Toshkent Meat Solutions — integratsiyalashgan go‘sht klasteri

Qayta ishlash sexi. Reja va jihozlar joylashuvi

Masshtab: 1:100

Bosqich	Varaq	Varaqlar
TEO oldi	11	19

Toshkent Meat Solutions Toshkent viloyati, 2026

Almashtirilgan inv. №

Imzo va sana

Ald nusxa inv. №