Ferma binolari fasadlari: sigirxona, g‘unajinxona, bo‘rdoqi bloki

Zamonaviy agrosanoat uslubi: antrasit metall, yog‘och lamellar, shaffof shtoralar; janubiy nishabda quyosh panellari

Sigirxona-1 va Sigirxona-2 — janubiy fasad · M 1:200

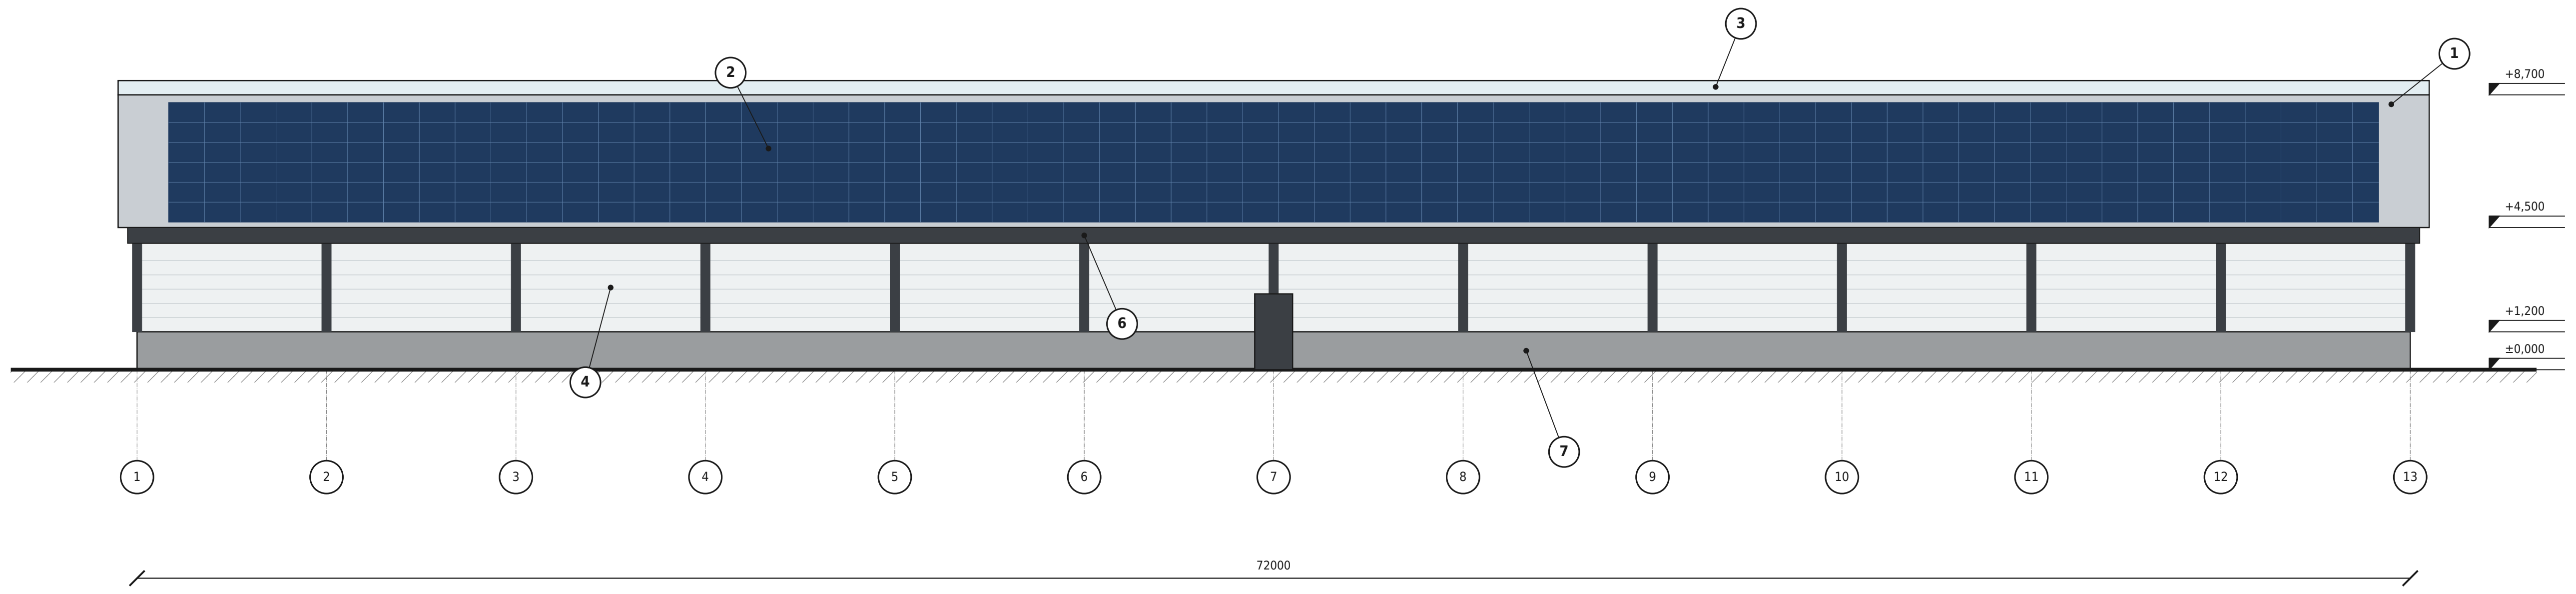
3
2
1
+8,700
+4,500
+1,200
±0,000
6
4
7
1
2
3
4
5
6
7
8
9
10
11
12
13
72000

Sigirxona — g‘arbiy torets fasad · M 1:100

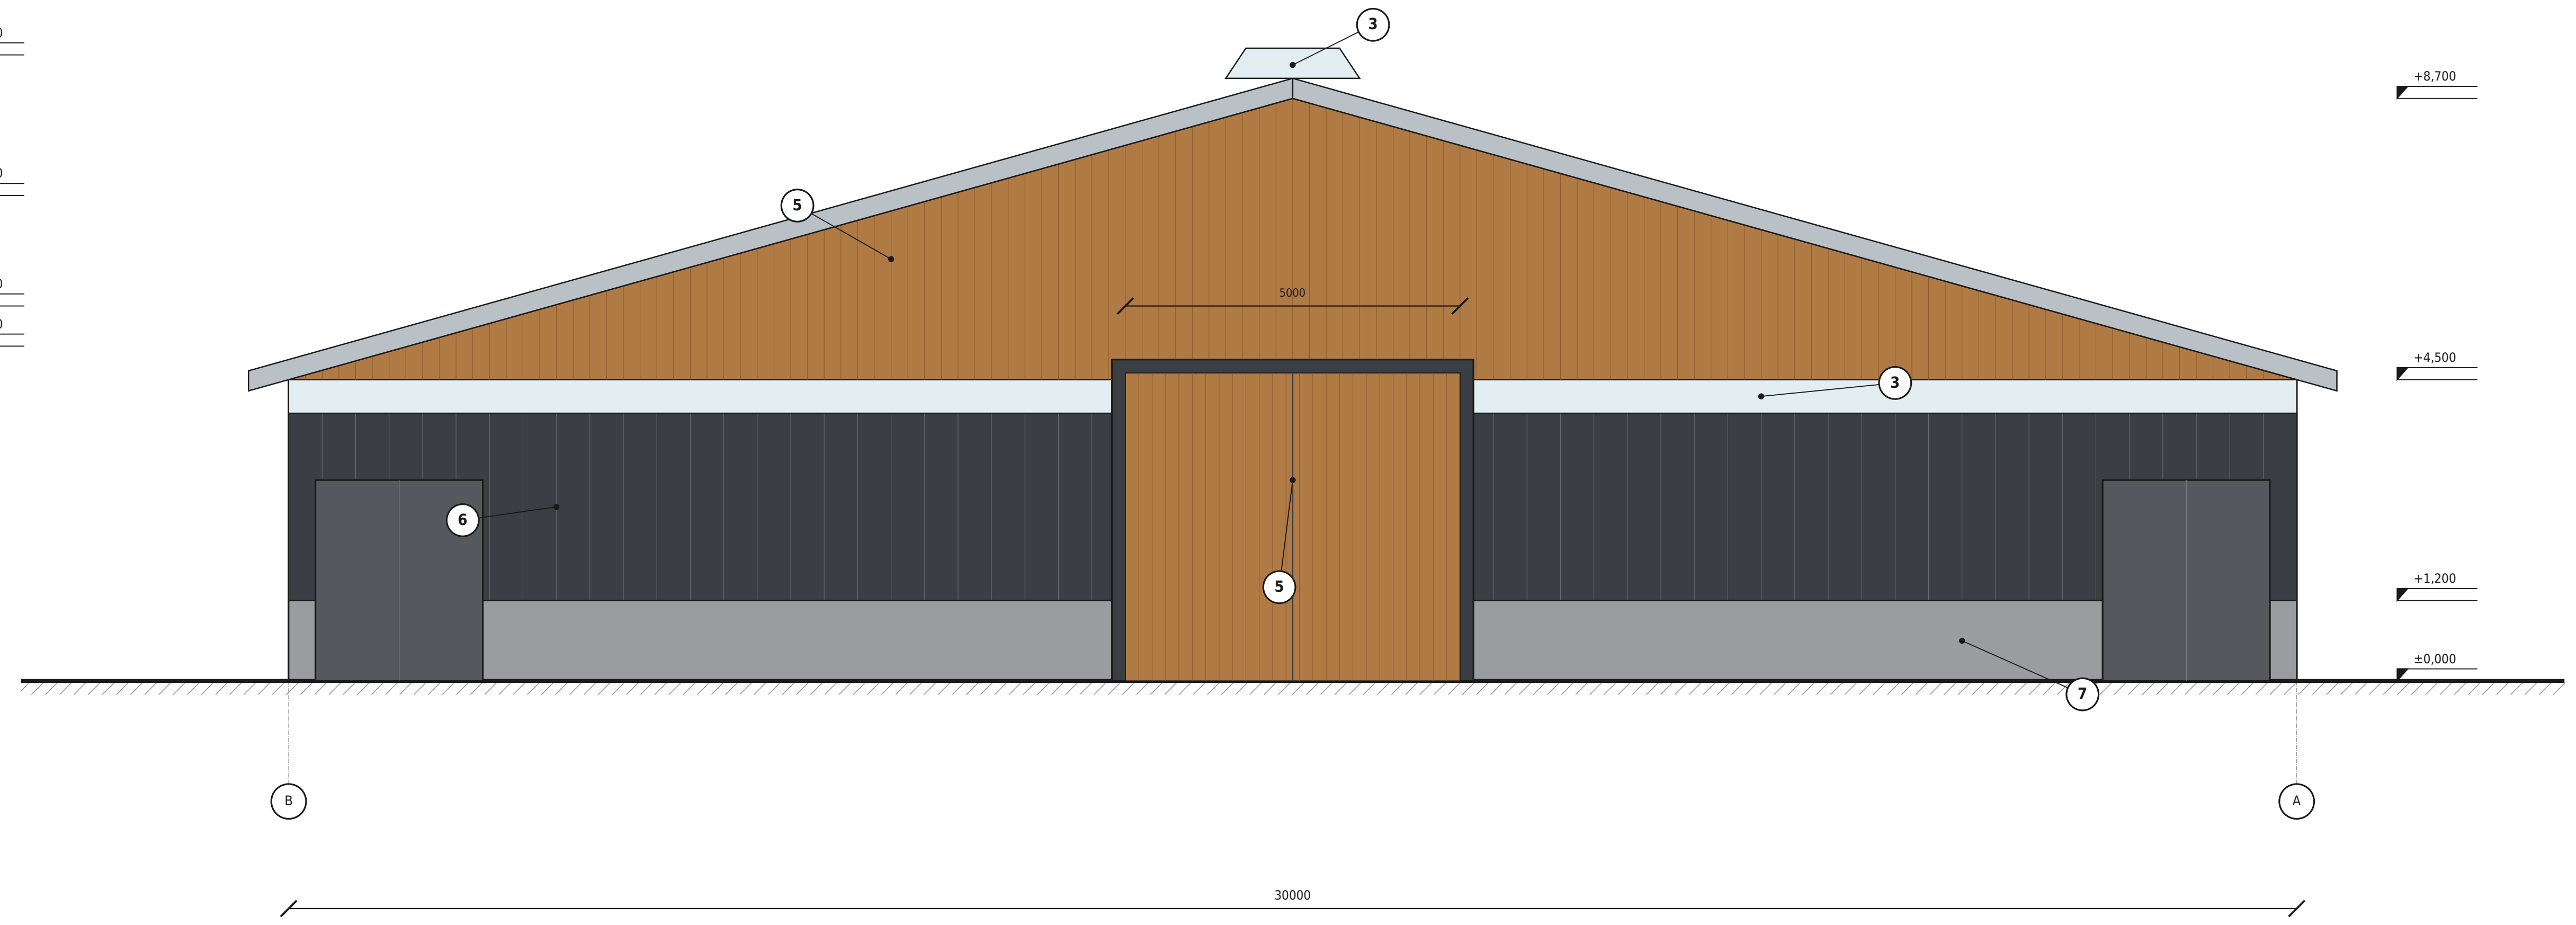
3
+8,700
5
5000
+4,500
3
6
5
+1,200
±0,000
7
B
A
30000

G‘unajinxona-1 va G‘unajinxona-2 — janubiy fasad · M 1:200

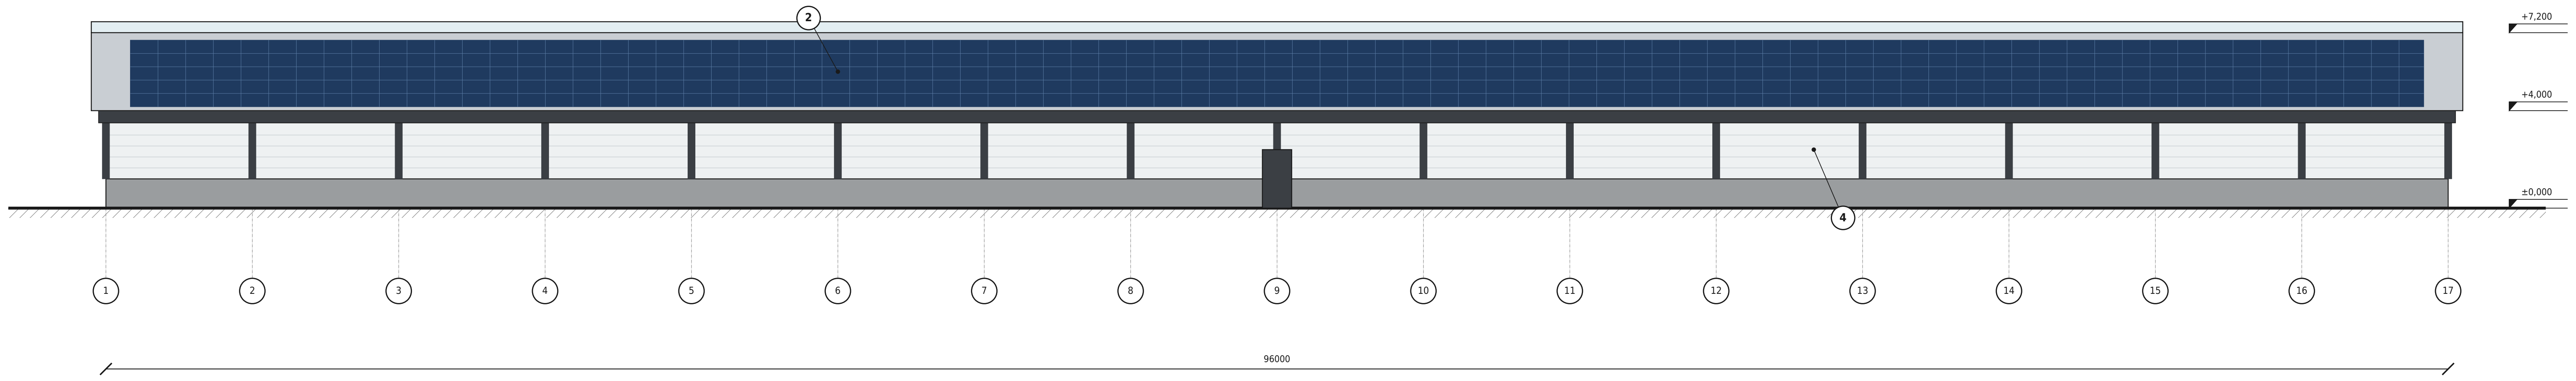
2
+7,200
+4,000
±0,000
4
1
2
3
4
5
6
7
8
9
10
11
12
13
14
15
16
17
96000

Bo‘rdoqi bloki — janubiy fasad · M 1:200

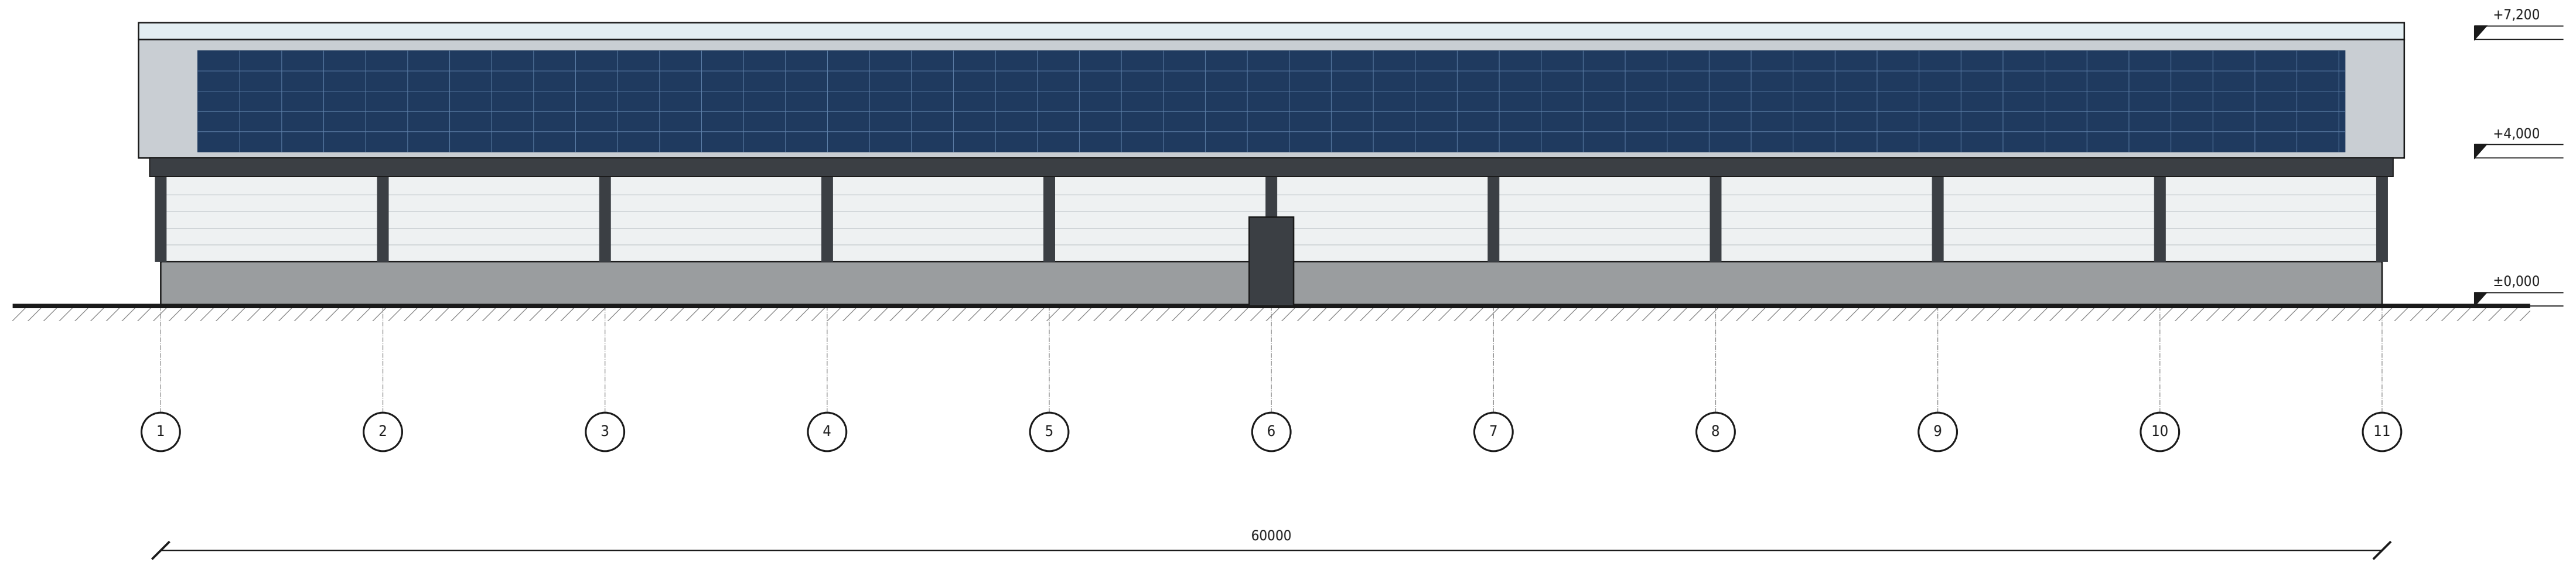
+7,200
+4,000
±0,000
1
2
3
4
5
6
7
8
9
10
11
60000

Materiallar va ranglar

1	■	Tom: kumushrang sendvich panel, RAL 9006
2	■	Quyosh panellari: monokristall, qora ramkali
3	■	Tom tirqishi va yorug‘lik polosasi: shaffof polikarbonat
4	▤	Yon shtora: oq yarim shaffof PVX mato, avtomatik
5	▥	Fasad lamellari: termoishlov berilgan qarag‘ay
6	■	Metall fasad panellari, rama, eshiklar: antrasit, RAL 7016
7	■	Sokol: antrasit rangli beton

Eslatmalar

1. Uzun fasadlar ochiq: yon shtoralar yozda ochiladi, qishda yopiladi; tabiiy shamollatish saqlanadi.
2. Quyosh panellari faqat janubiy nishabda (14-varaq); shimoliy nishab va qirradagi tirqish ochiq.
3. Torets fasadlarda pastki qism antrasit metall, yuqori uchburchak — yog‘och lamellar.
4. G‘unajinxona va bo‘rdoqi bloki toretslari sigirxonaniki bilan bir xil uslubda (24 m oraliq).
5. Balandlik belgilari 5- va 7-varaqlardagi kesimlarga mos; ranglar shartli, ishchi loyihada aniqlanadi.

Almashtirilgan inv. №

Imzo va sana

Asl nusxa inv. №

O‘zg.	Varaq	Hujjat №	Imzo	Sana
Ishlab chiqdi				10.2026
Tekshirdi				10.2026
Bosh muhandis				10.2026
Normativ nazorat				10.2026
Tasdiqladi				10.2026

TMS-2026-TEO

Toshkent Meat Solutions — integratsiyalashgan go‘sht klasteri

Ferma binolari fasadlari: sigirxona, g‘unajinxona, bo‘rdoqi bloki

Masshtab: 1:200, 1:100

Bosqich	Varaq	Varaqlar
TEO oldi	16	19

Toshkent Meat Solutions
Toshkent viloyati, 2026