Ferma: sog‘ish zali va ma’muriy bino fasadlari

Fermaning ko‘rgazmali binolari: yog‘och va antrasit, karusel ustida yorug‘lik fonari, tomda quyosh panellari

Sog‘ish zali va sut bloki — sharqiy fasad · M 1:100

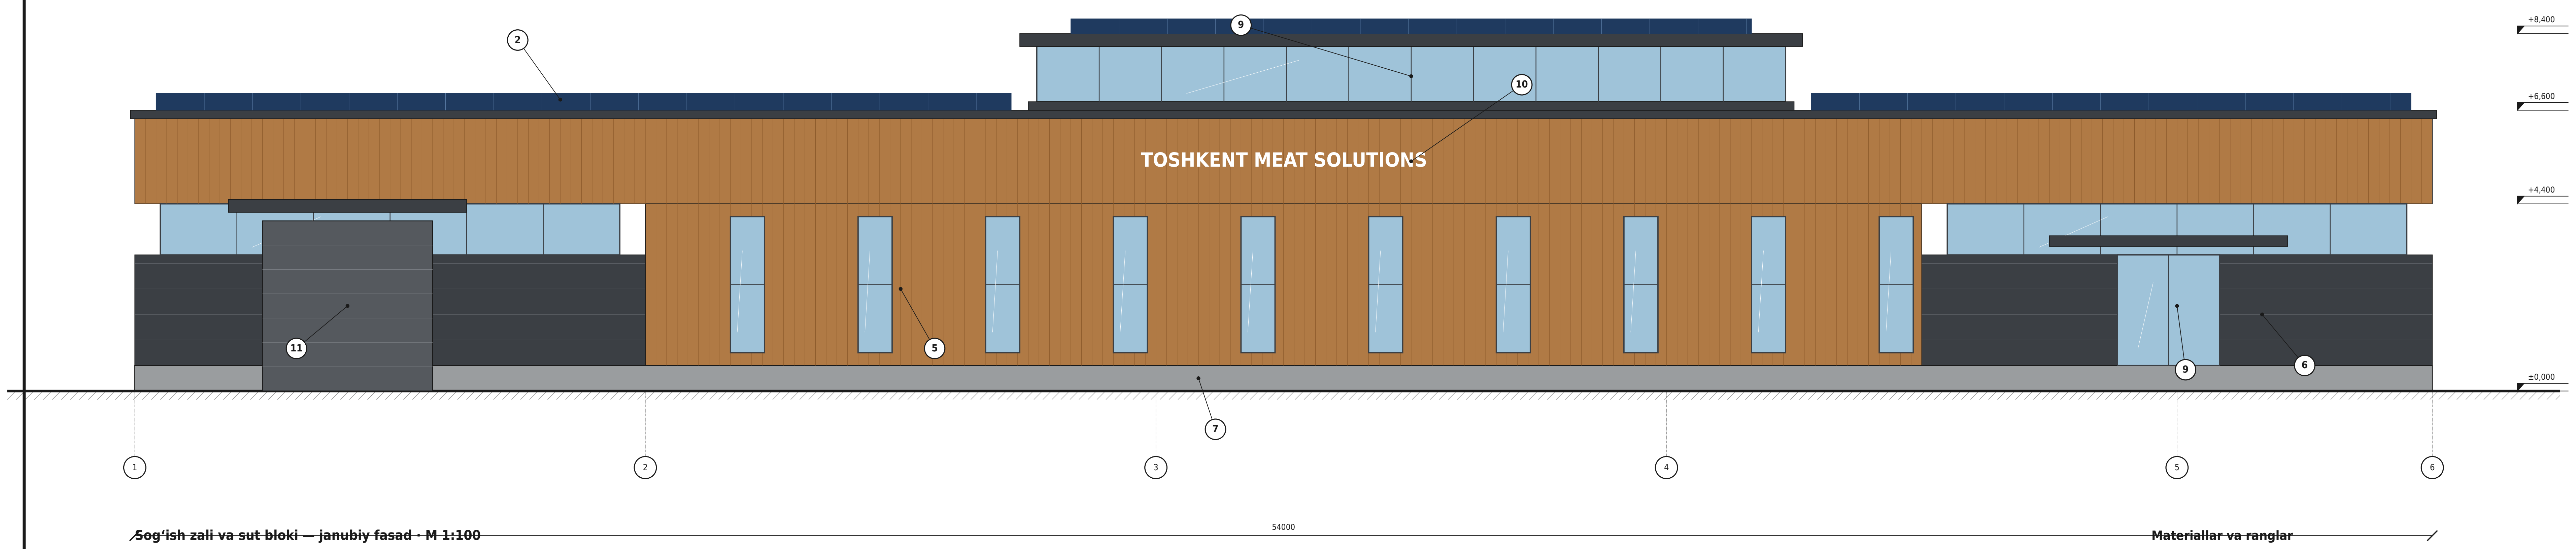

Sog‘ish zali va sut bloki — janubiy fasad · M 1:100

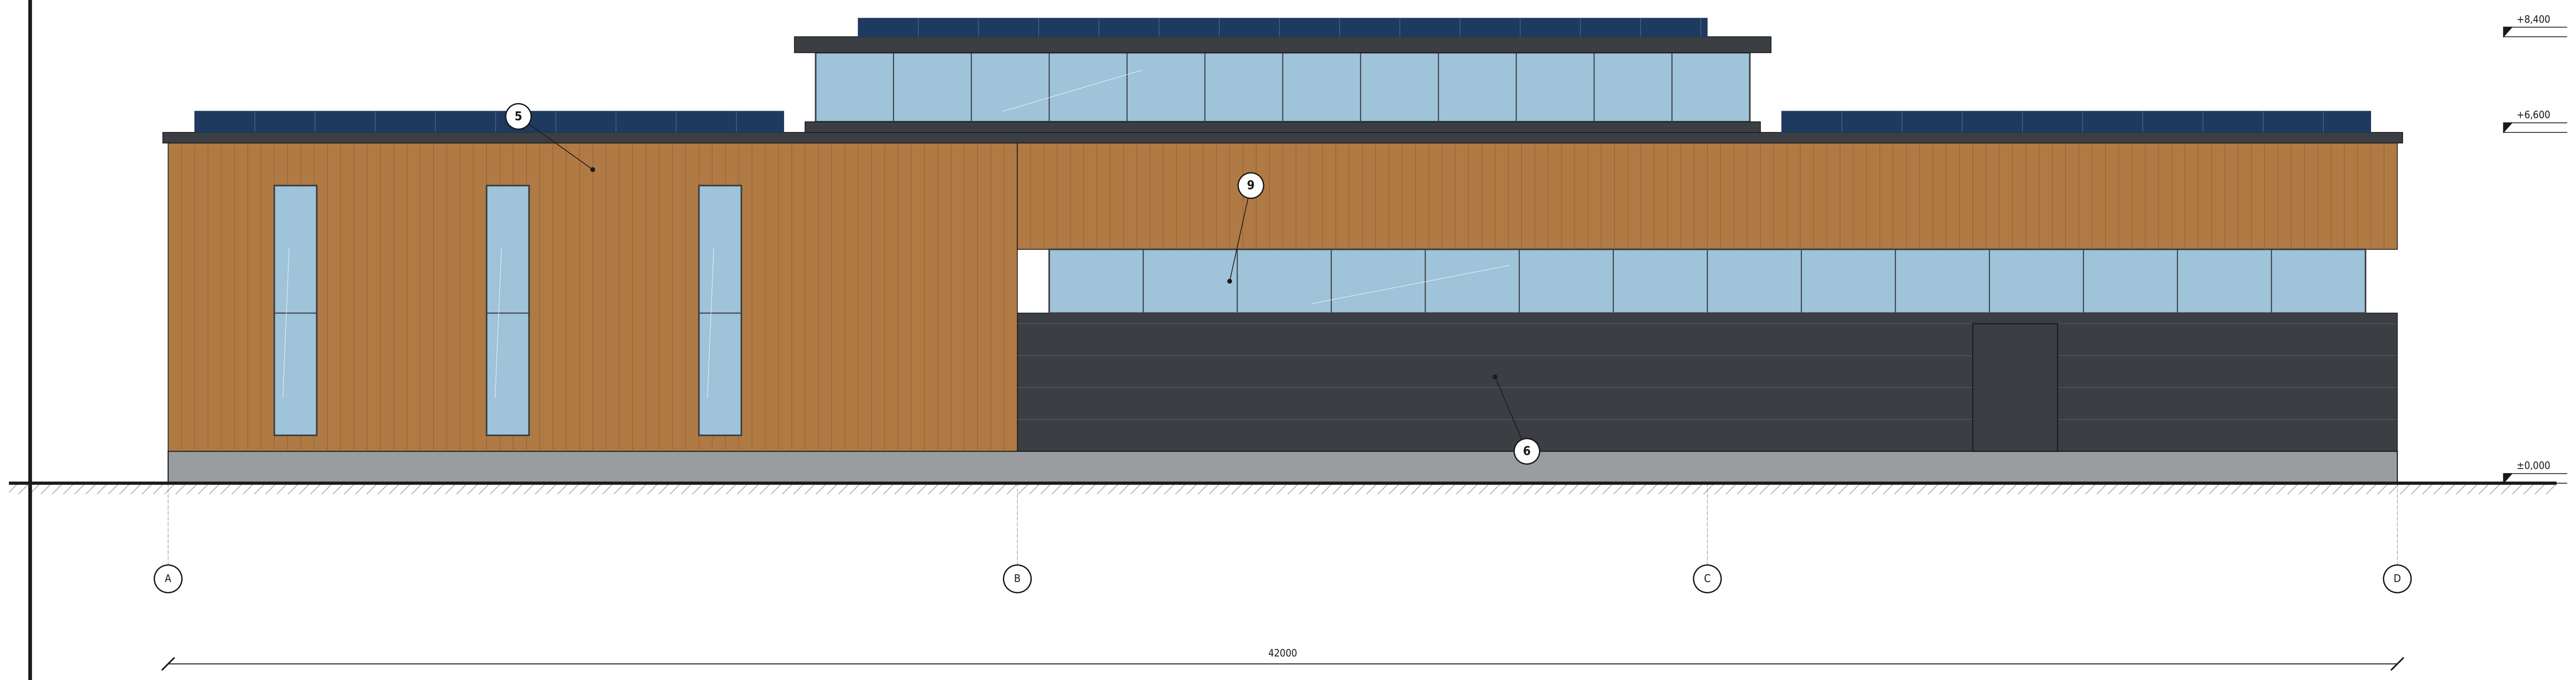

Materiallar va ranglar

2	🟦	Quyosh panellari: monokristall, qora ramkali
5	🟫	Fasad lamellari: termoishlov berilgan qarag‘ay
6	⬛	Metall fasad panellari, rama, eshiklar: antrasit, RAL 7016
7	⬛	Sokol: antrasit rangli beton
9	🟦	Vitraj: alyuminiy profil, past emissiyali shisha
10	⬜	Brend yozuvi: hajmli harflar, kechqurun yoritiladi
11	⬛	Seksiyali darvoza va dok-shelter

Eslatmalar

1. Karusel ustidagi 18 × 18 m yorug‘lik fonari zalga tabiiy yorug‘lik beradi.
2. Tekis tomlarda quyosh panellari sharq–g‘arb 10° (14-varaq); parapet ustidan qisman ko‘rinadi.
3. Sharqiy fasadda sut mashinasi uchun darvoza (4 × 4 m) va mehmonlar kirishi.
4. Fasadlar 6-varaq rejasiga konseptual mos; 6-varaq bosh rejaga moslab qayta chizilgach, teshiklar joyi aniqlanadi.
5. Balandliklar konseptual, ishchi loyihada hisob bilan aniqlanadi.

Ma’muriy-maishiy bino (sanitariya o‘tkazgichi bilan) — janubiy fasad · M 1:100

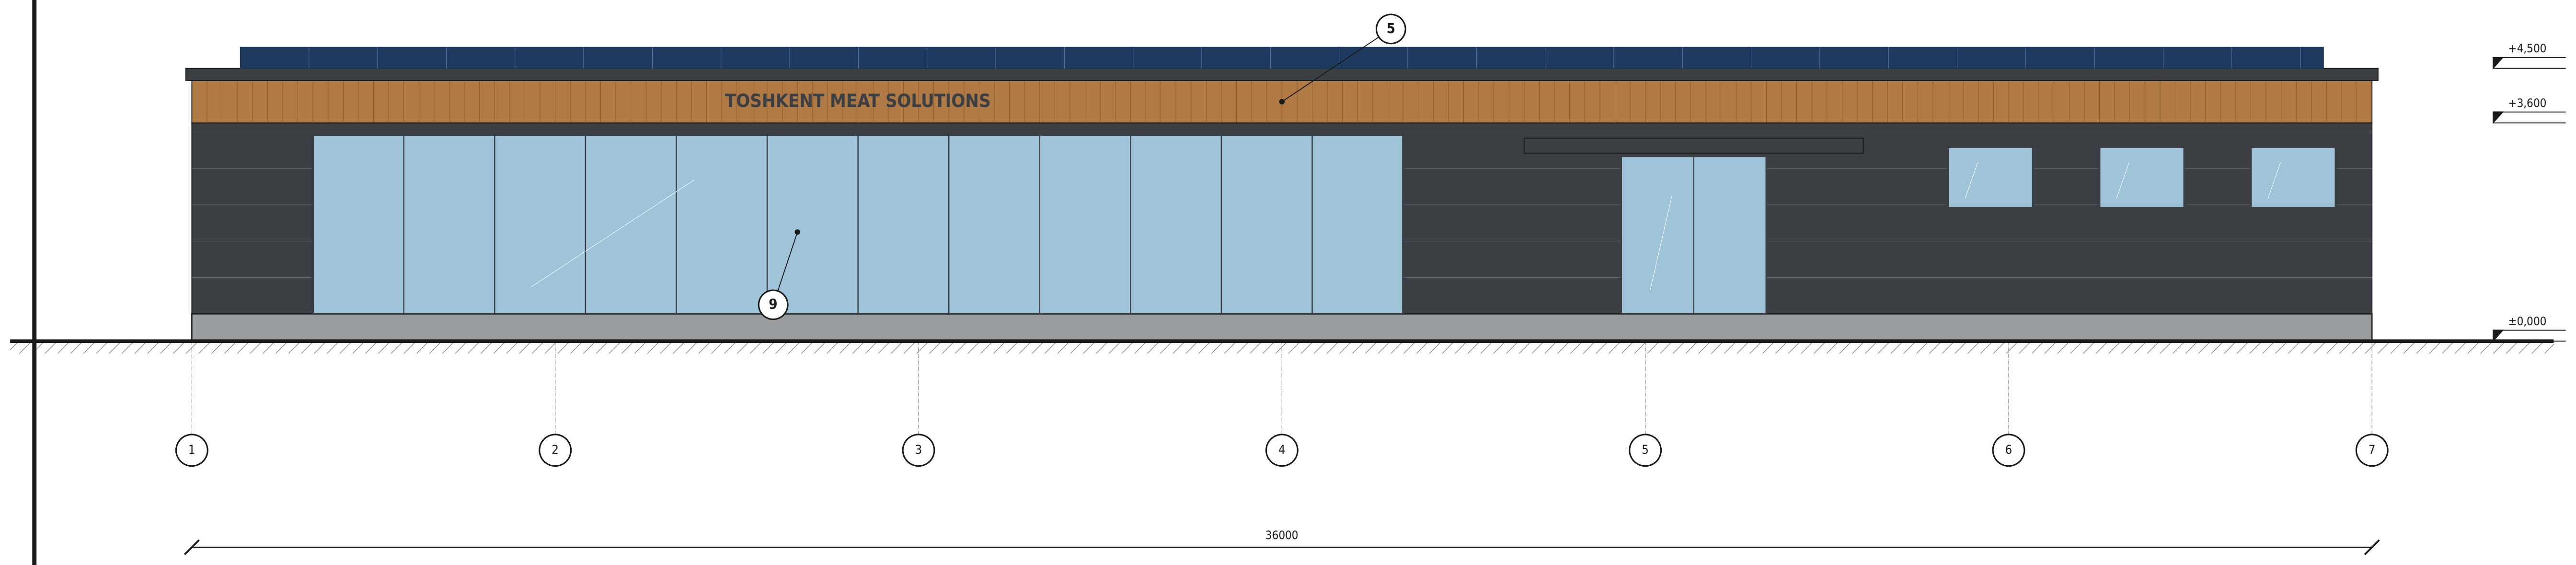

Almashtirilgan inv. №

Imzo va sana

Asl nusxa inv. №

O‘zg.	Varaq	Hujjat №	Imzo	Sana
Ishlab chiqdi				10.2026
Tekshirdi				10.2026
Bosh muhandis				10.2026
Normativ nazorat				10.2026
Tasdiqladi				10.2026

TMS-2026-TEO

Toshkent Meat Solutions — integratsiyalashgan go‘sht klasteri

Sog‘ish zali va ma’muriy bino (ferma) fasadlari

Masshtab: 1:100

Bosqich	Varaq	Varaqlar
TEO oldi	17	19

Toshkent Meat Solutions
Toshkent viloyati, 2026