1-maydon bosh rejasi: to‘rtburchak dalalar, tomchilatib sug‘orish, ferma va ilmiy markaz · 419,0 ga

M 1:5000. O‘lchamlar metrda

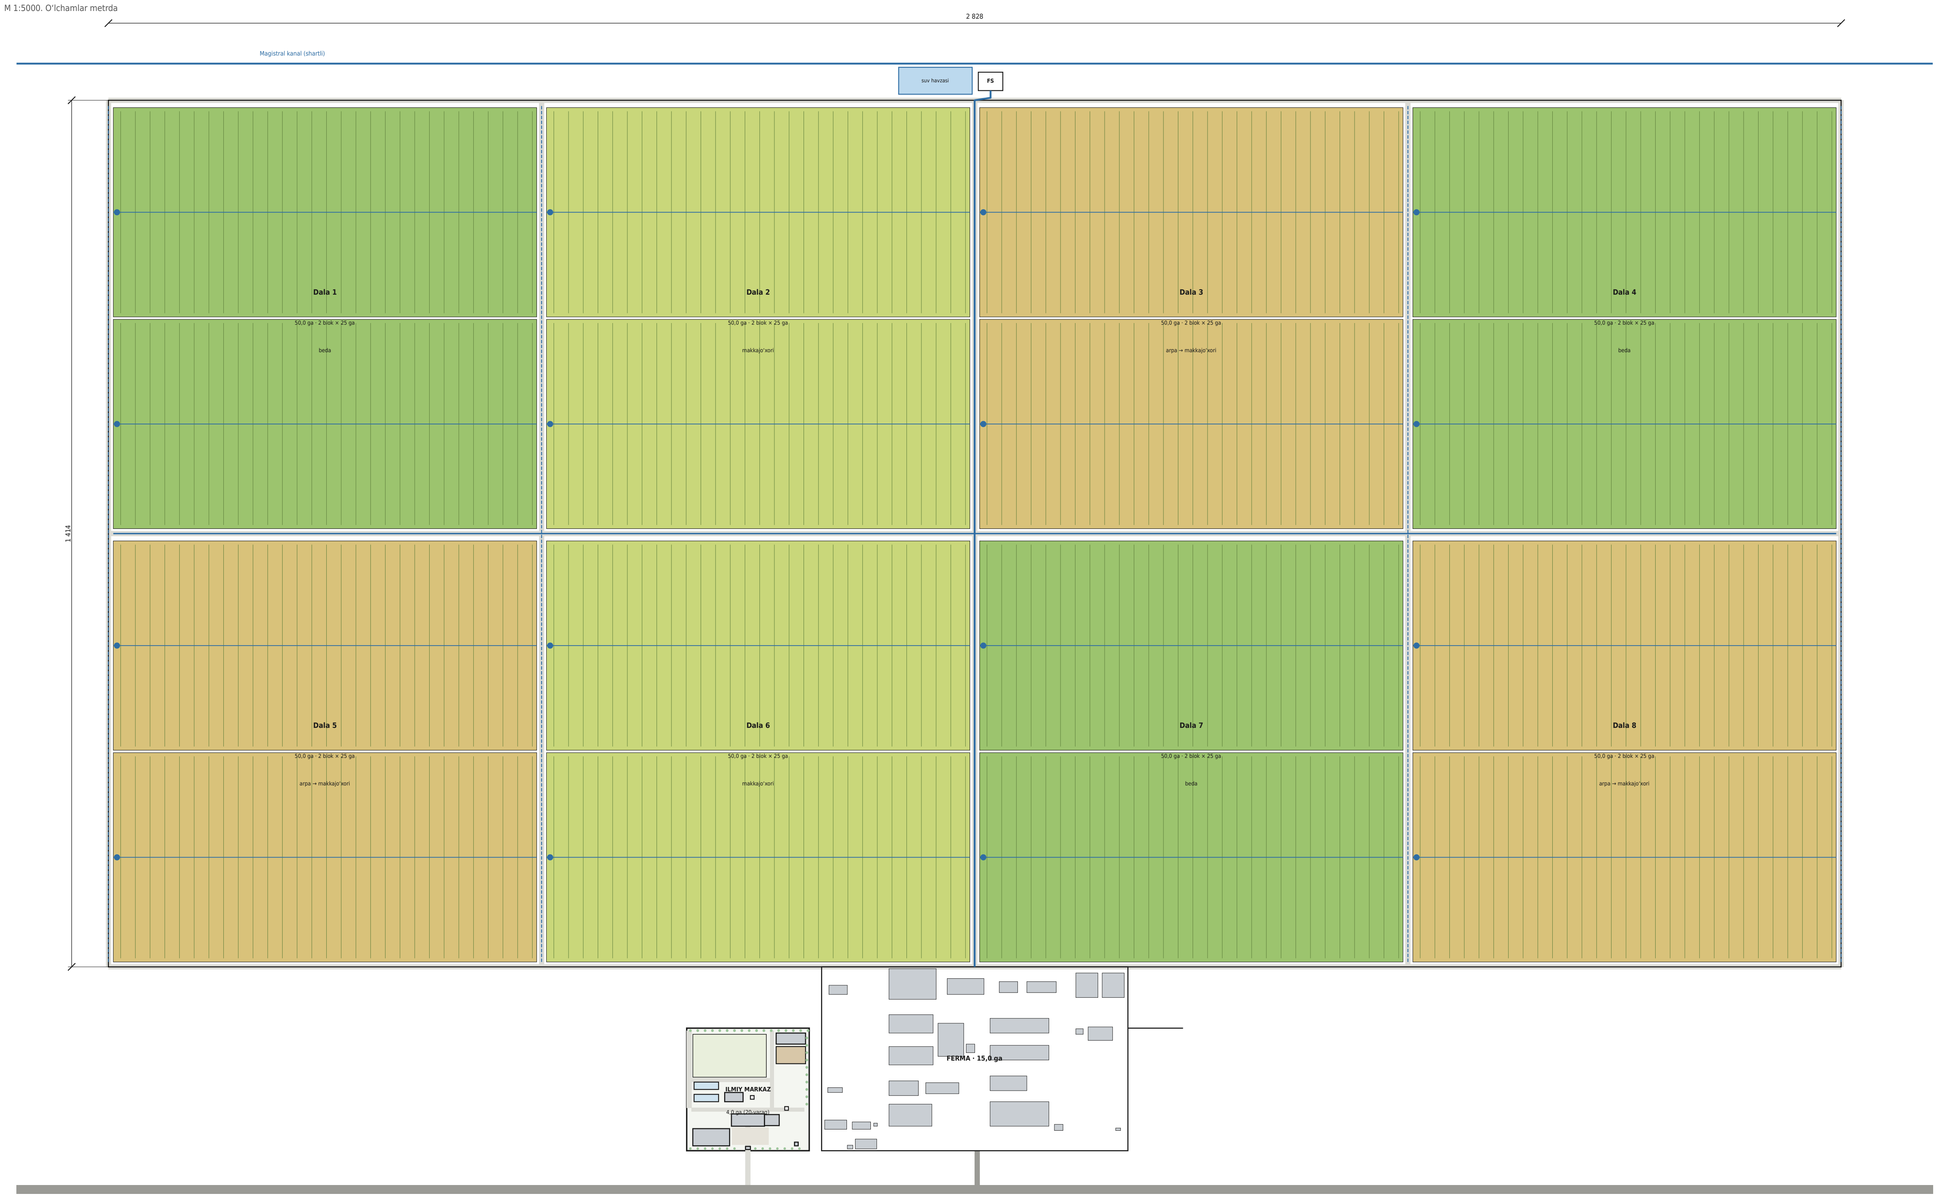

Ekinlar tuzilmasi (tomchilatib sug‘orish)

Ekin (o‘rtacha almashlab ekish)	Maydon, ga	Hosil
Beda (pichan, 4–5 o‘rim), yer osti tomchilatib	140	14 t/ga
Makkajo‘xori silos	100	55 t/ga
Kuzgi arpa (don + somon)	160	6 + 3,5 t/ga
Takroriy makkajo‘xori silos (arpadan keyin)	120	40 t/ga

Yer balansi

Maydon tarkibi	ga	%
Ekin maydoni (8 dala × 50,0 ga)	400,0	95,47
shu jumladan ekiladigan bloklar (16 × 24,4)	390,6	
dala yo‘llari, quvur trassalari	9,4	
Ferma (500 × 300 m)	15,0	3,58
Ilmiy-innovatsion markaz (200 × 200 m)	4,0	0,95
Jami 1-maydon	**419,0**	**100**

Eslatmalar

1. Dalalar to‘rtburchak, butun maydon ekiladi; har bir dala 2 ta 25 ga lik tomchilatib sug‘orish blokiga bo‘lingan (16 blok).
2. Suv kanaldan suv havzasiga, keyin filtrlash va fertigatsiya stansiyasidan (FS) magistral quvur orqali bloklarga beriladi.
3. Bloklarda tomchilatgich tasmalar shimol–janub yo‘nalishida; har blokda avtomat klapan va tuproq namligi datchigi.
4. Dorilash va monitoring agrodronlar bilan (13-varaq); ferma va ilmiy markaz massivning janubiy chetida, yo‘l bo‘yida.
5. Kanal, yo‘l va elektr liniyasi shartli ko‘rsatilgan; massiv tanlangach aniqlanadi.

O‘zg.	Varaq	Hujjat №	Imzo	Sana
Ishlab chiqdi				10.2026
Tekshirdi				10.2026
Bosh muhandis				10.2026
Normativ nazorat				10.2026
Tasdiqladi				10.2026

MS-2026-TEO

Meat Solutions — integratsiyalashgan go‘sht klasteri

1-maydon bosh rejasi: ekin maydoni, ferma va ilmiy markaz (419,0 ga)

Masshtab: 1:5000

Bosqich	Varaq	Varaqlar
TEO oldi	3	21

Meat Solutions
Toshkent viloyati, 2026

Almashtirilgan inv. №

Inqiz va sana

Asl nusxa inv. №