

Yosh mollar binolari: g‘unajinxona, bo‘rdoqi bloki, buzoqxona

Rejalar M 1:200, kesim M 1:100. O‘lchamlar millimetrda (4-varaq, 13, 15, 16, 17-pozitsiyalar)


G‘unajinxona (300 joy) · 96 × 24 m · ikki bino

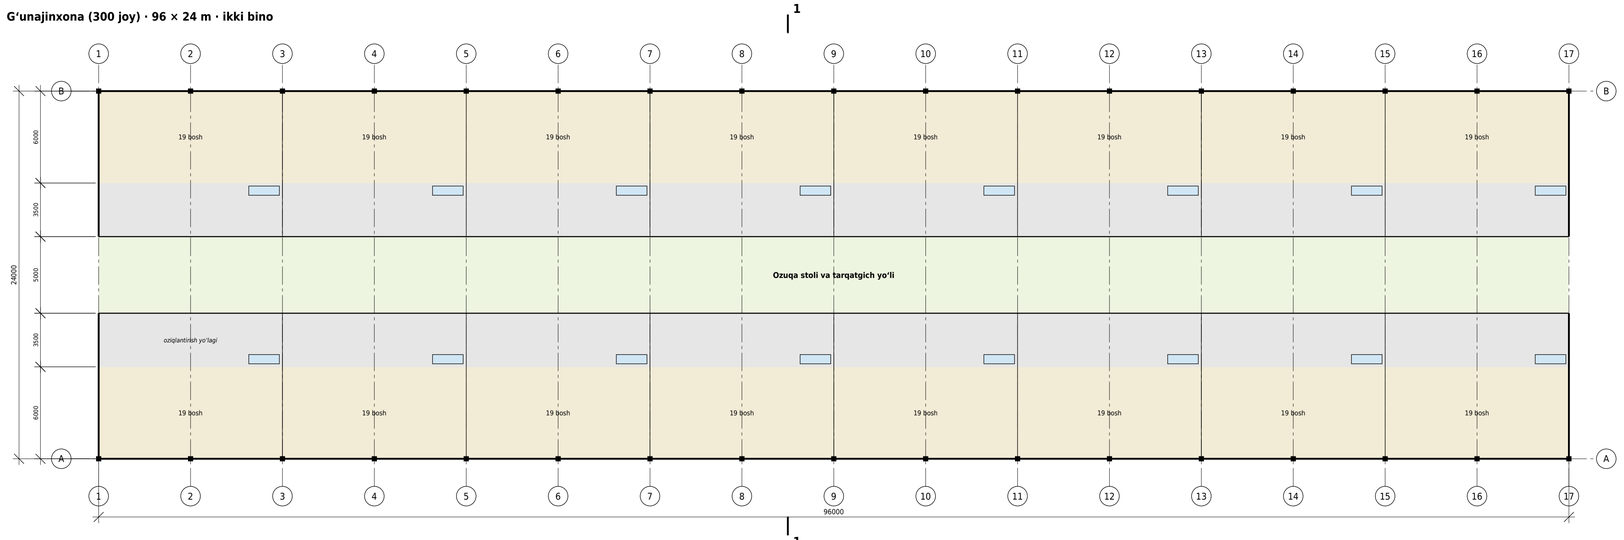


Bo‘rdoqi bloki (240 joy) · 60 × 24 m

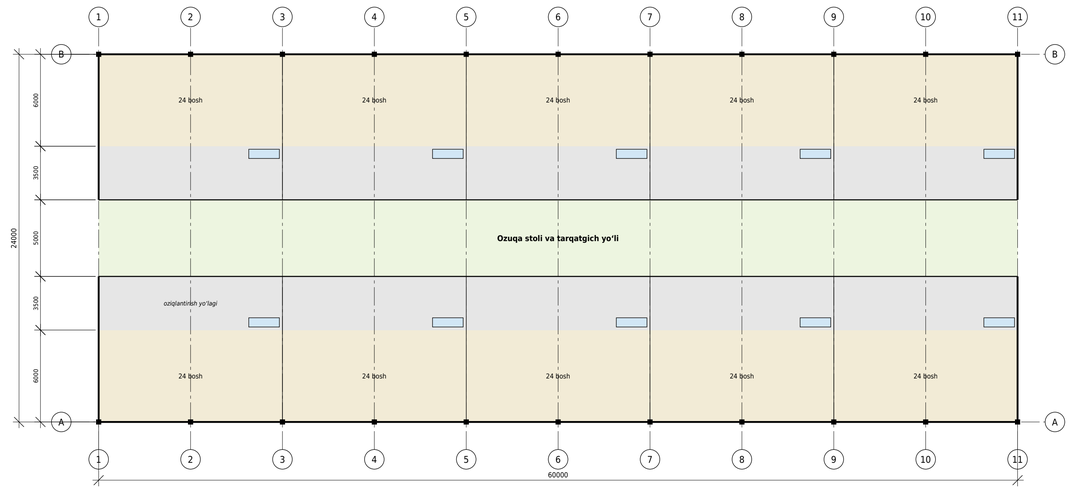

Buzoqxona (160 joy) · 54 × 18 m

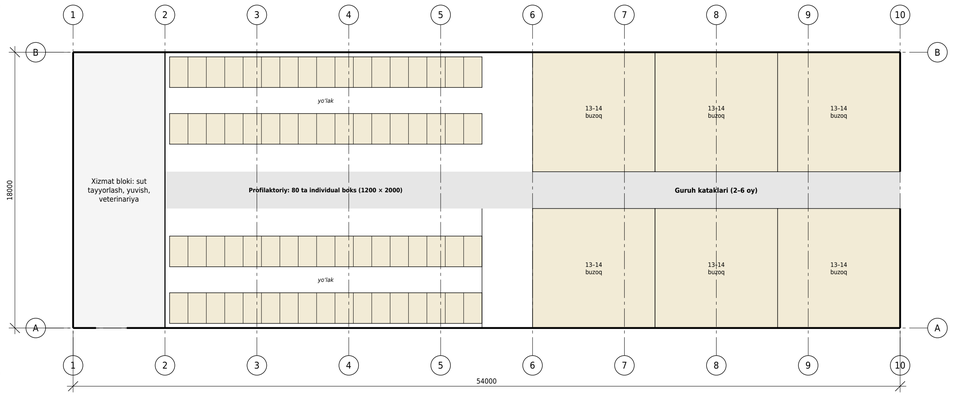

1–1 kesim (g‘unajinxona). M 1:100

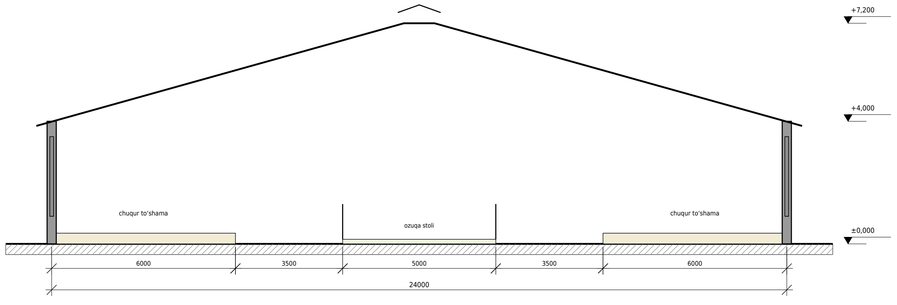

Asosiy ko‘rsatkichlar

Bino	O‘lcham, m	Joy	Maydon, m²
G‘unajinxona-1	96 × 24	300	2 304
G‘unajinxona-2	96 × 24	300	2 304
Bo‘rdoqi bloki	60 × 24	240	1 440
Buzoqxona	54 × 18	160	972

Eslatmalar

1. G‘unajin va bo‘rdoqi kataklari chuqur to‘shamali (somon); bir boshga 6,0 va 4,75 m² to‘shama to‘g‘ri keladi.
2. Bo‘rdoqi yiliga 1,5 aylanma bilan ≈ 360 bosh beradi va qushxonaga yuboriladi.
3. Buzoqlar 0–2 oyligida individual boksda, keyin guruh kataklarida saqlanadi.

O‘zg.	Varaq	Hujjat №	Imzo	Sana
Ishlab chiqdi				10.2026
Tekshirdi				10.2026
Bosh muhandis				10.2026
Normaviy nazorat				10.2026
Tasdiqladi				10.2026

MS-2026-TEO

Meat Solutions — integratsiyalashgan go‘sht klasteri

G‘unajinxona, bo‘rdoqi bloki, buzoqxona. Rejalar va kesim

Masshtab: 1:200, 1:100

Bosqich	Varaq	Varaqlar
TEO oldi	7	21

Meat Solutions
Toshkent viloyati, 2026

Almashtirilgan inv. №

Imzo va sana

Asl nusxa inv. №