

Muzlatgich va sovutish markazi · 3 000 t · 84 × 48 m

Reja va kesim M 1:200. O‘lchamlar millimetrda. Sovutilgan 600 t, muzlatilgan 2 000 t, tayyor mahsulot 400 t; shok-muzlatish 40 t/sutka

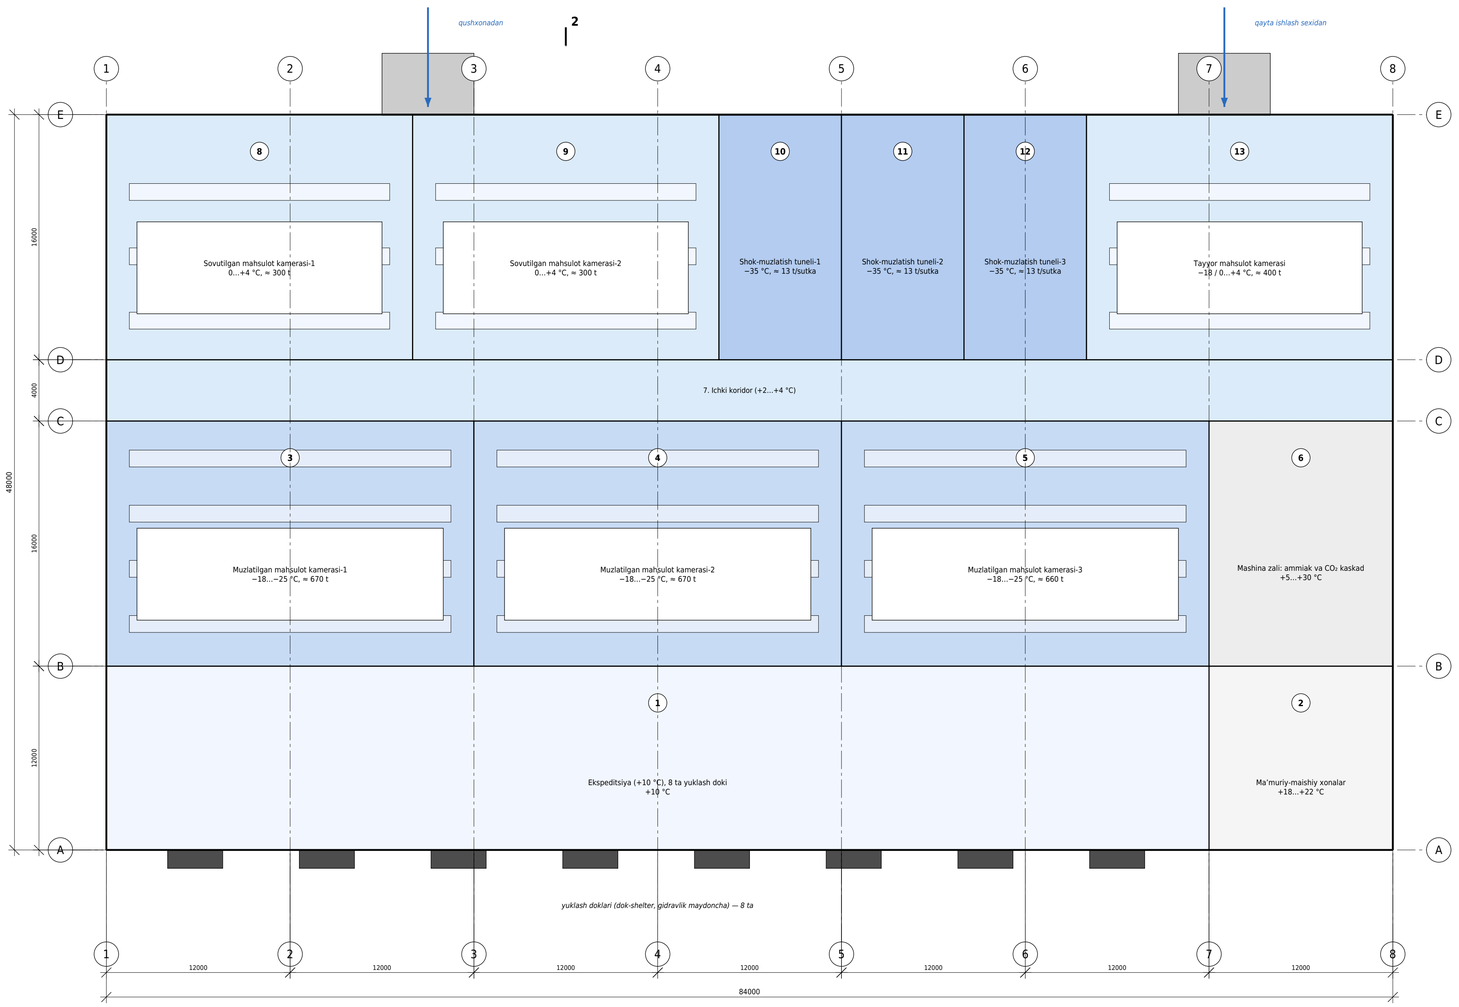

2

2–2 kesim. M 1:200

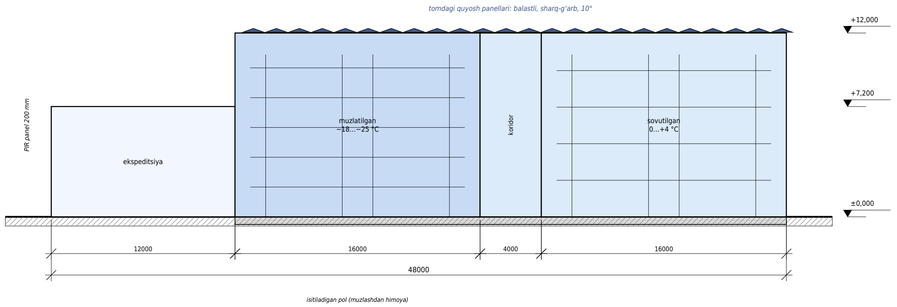

Xonalar eksplikatsiyasi

№	Xona	Harorat, °C	Sig‘im
1	Ekspeditsiya (+10 °C), 8 ta yuklash doki	+10	
2	Ma’muriy-maishiy xonalar	+18…+22	
3	Muzlatilgan mahsulot kamerasi-1	−18…−25	≈ 670 t
4	Muzlatilgan mahsulot kamerasi-2	−18…−25	≈ 670 t
5	Muzlatilgan mahsulot kamerasi-3	−18…−25	≈ 660 t
6	Mashina zali: ammiak va CO_2 kaskad	+5…+30	
7	Ichki koridor	+2…+4	
8	Sovutilgan mahsulot kamerasi-1	0…+4	≈ 300 t
9	Sovutilgan mahsulot kamerasi-2	0…+4	≈ 300 t
10	Shok-muzlatish tuneli-1	−35	≈ 13 t/sutka
11	Shok-muzlatish tuneli-2	−35	≈ 13 t/sutka
12	Shok-muzlatish tuneli-3	−35	≈ 13 t/sutka
13	Tayyor mahsulot kamerasi	−18 / 0…+4	≈ 400 t

Eslatmalar

1. Sovutish: ammiak va CO_2 kaskad tizimi, chastota o‘zgartirgichli kompressorlar; freonsiz.
2. Devor va tom: PIR sendvich panellar 200 mm (muzlatilgan kameralar), 150 mm (sovutilgan).
3. Kompressor issiqligidan 60–70 °C issiq suv olinadi va qushxonaga beriladi.
4. Kunduzi quyosh energiyasi ko‘p paytda kameralar 1–2 °C pastroq sovutiladi.
5. Stellajlar: muzlatilgan kameralarda 5 qavat, sovutilgan kameralarda 4 qavat.

O‘zg.	Varaq	Hujjat №	Imzo	Sana
Ishlab chiqdi				10.2026
Tekshirdi				10.2026
Bosh muhandis				10.2026
Normativ nazorat				10.2026
Tasdiqladi				10.2026

MS-2026-TEO

Meat Solutions — integratsiyalashgan go‘sht klasteri

Muzlatgich (3 000 t). Reja va 2–2 kesim

Masshtab: 1:200

Bosqich	Varaq	Varaqlar
TEO oldi	**10**	21

Meat Solutions
Toshkent viloyati, 2026

Almashtirilgan inv. №

Imzo va sana

Asl nusxa inv. №