Qushxona binosi va qayta ishlash sexi fasadlari

Oziq-ovqat sanoati binolari: oq sendvich panellar, antrasit sokol va parapet, xodimlar kirishida vitraj, tomda quyosh panellari

Qushxona binosi — janubiy fasad · M 1:200

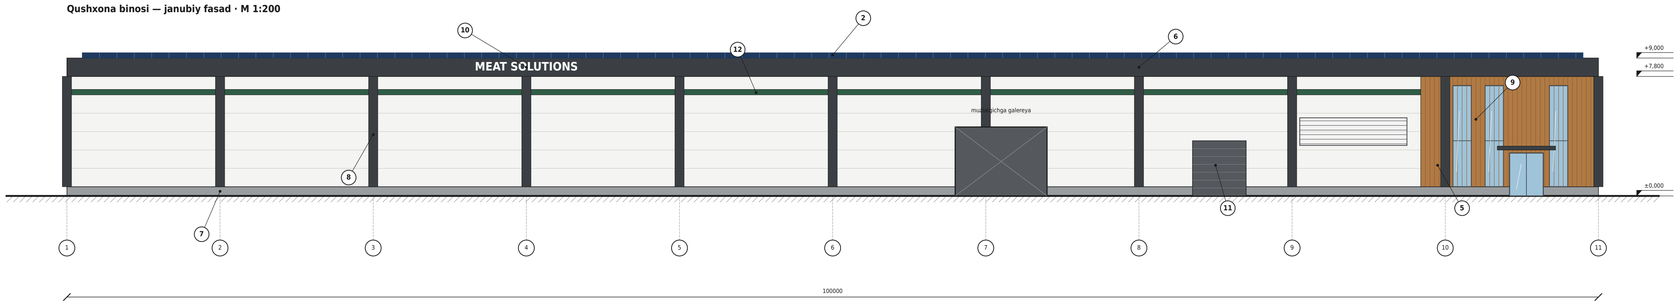

Qushxona binosi — sharqiy fasad · M 1:200

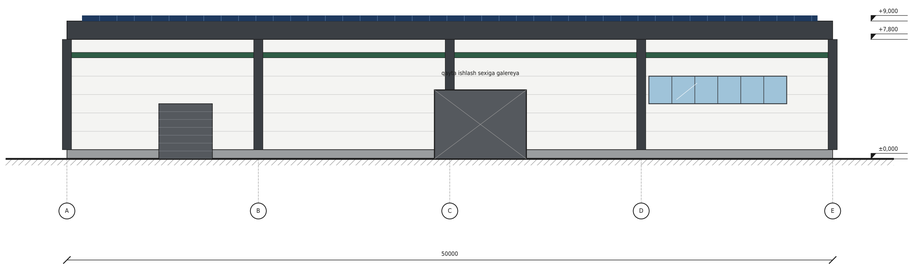

Qayta ishlash sexi — janubiy fasad · M 1:200

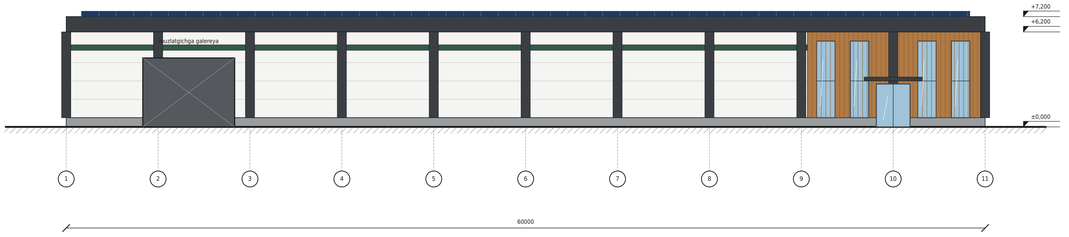

Qushxona binosi — g‘arbiy fasad (chorva kirishi) · M 1:200

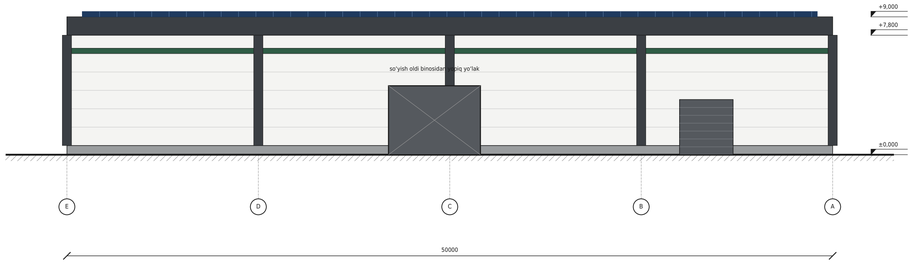

Materiallar va ranglar

2		Quyosh panellari: monokristall, qora ramkali
5		Fasad lamellari: termoishlov berilgan qarag‘ay
6		Metall fasad panellari, rama, eshiklar: antrasit, RAL 7016
7		Sokol: antrasit rangli beton
8		Oq sendvich panel, RAL 9010 (oziq-ovqat sanoati uchun)
9		Vitraj: alyuminiy profil, past emissiyali shisha
10		Brend yozuvi: hajmli harflar, kechqurun yoritiladi
11		Seksiyali darvoza va dok-shelter
12		Aksent polosa va pilyastrlar: to‘q yashil RAL 6005 / antrasit

Eslatmalar

1. Tashqi devorlar oziq-ovqat sanoati uchun oq sendvich panellardan; ichki tomoni yuviladigan qoplamali.
2. Parapet antrasit, uning ortida tekis tomda sharq–g‘arb quyosh panellari (15-varaq) qisman ko‘rinadi.
3. Xodimlar kirishi janubi-sharqda, vitraj va soyabon bilan; texnik darvozalar alohida.
4. Galereyalar 8- va 9-varaqlar bilan moslashtirilgach, kesib ko‘rsatilgan joylari aniqlanadi.
5. Balandliklar konseptual: qushxona +9,000 (osma yo‘l balandligi hisobiga), qayta ishlash sexi +7,200.

					MS-2026-TEO	
					Meat Solutions — integratsiyalashgan go‘sht klasteri	
					Qushxona binosi va qayta ishlash sexi fasadlari	
O‘zg.	Varaq	Hujjat №.	Imzo	Sana		
Ishlab chiqdi				10.2026	Massshtab: 1:200	
Tekshirdi				10.2026		
Bosh muhandis				10.2026		
Normativ nazorat				10.2026		
Tasdiqladi				10.2026		

Bosqich	Varaq	Varaqlar
TEO oldi	18	21

Meat Solutions
Toshkent viloyati, 2026

Almashtirilgan inv. №

Imzo va sana

Asl nusxa inv. №