Muzlatgich va qushxona majmuasi ma’muriy binosi fasadlari

Muzlatgich: oq PIR panellar, 8 ta yuklash doki; ma’muriy bino: vitraj, yog‘och lamellar, antrasit — majmuaning yuzi

Muzlatgich — janubiy fasad · M 1:200

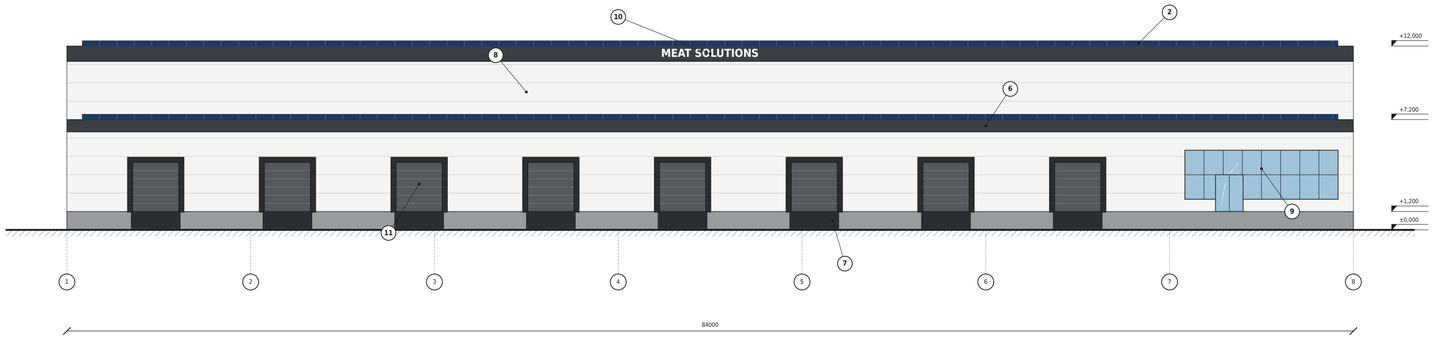

Muzlatgich — sharqiy fasad · M 1:200

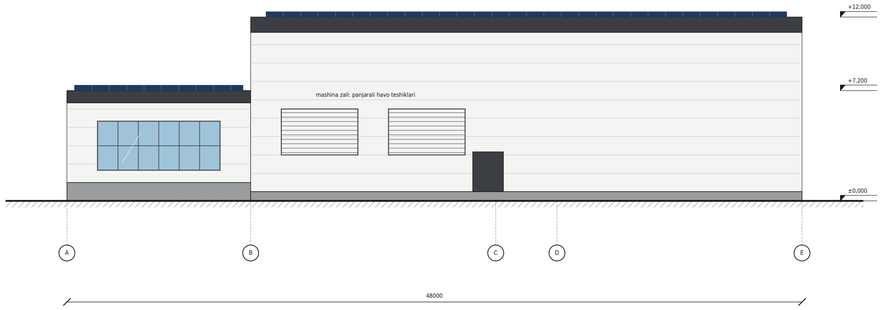

Ma’muriy bino (2 qavat) — janubiy fasad · M 1:100

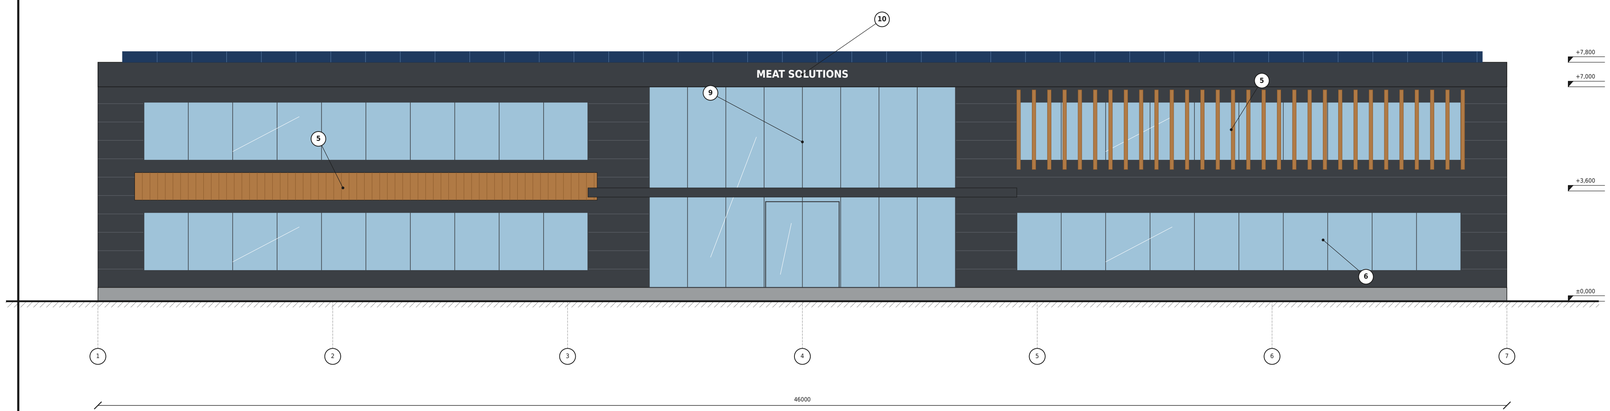

Materiallar va ranglar

2		Quyosh panellari: monokristall, qora ramkali
5		Fasad lamellari: termoishlov berilgan qarag‘ay
6		Metall fasad panellari, rama, eshiklar: antrasit, RAL 7016
7		Sokol: antrasit rangli beton
8		Oq sendvich panel, RAL 9010 (oziq-ovqat sanoati uchun)
9		Vitraj: alyuminiy profil, past emissiyali shisha
10		Brend yozuvi: hajmli harflar, kechqurun yoritiladi
11		Seksiyali darvoza va dok-shelter

Eslatmalar

1. Muzlatgich devorlari PIR panel: 200 mm (muzlatilgan), 150 mm (sovutilgan); ichki ko‘rinish 10-varaqda.
2. 8 ta dok: dok-shelter, gidravlik maydoncha, +1,200.
3. Tomlarda quyosh panellari (15-varaq), parapet ortidan qisman ko‘rinadi.
4. Ma’muriy bino — majmuaning bosh fasadi: kirish vitraji, yog‘och soyabon-lamellar.
5. Balandliklar konseptual.

Almashtirilgan inv. №

Imzo va sana

Asl nusxa inv. №

					MS-2026-TEO		
					Meat Solutions — integratsiyalashgan go‘sht klasteri		
					Muzlatgich va qushxona ma’muriy binosi fasadlari		
O‘zg.	Varaq	Hujjat №.	Imzo	Sana			
Ishlab chiqdi				10.2026	Masshtab: 1:200, 1:100	Bosqich	Varaq	Varaqlar
Tekshirdi				10.2026		TEO oldi	19	21
Bosh muhandis				10.2026				
Normativ nazorat				10.2026		Meat Solutions Toshkent viloyati, 2026		
Tasdiqladi				10.2026				