Ilmiy-innovatsion markaz bosh rejasi · 4,0 ga (200 × 200 m)

5 qavatli ilmiy-laboratoriya minorasi, 100 ta ish o‘rni: naslchilik va dehqonchilik tadqiqotlari, yangiliklarni joriy etish, fermerlarni o‘qitish

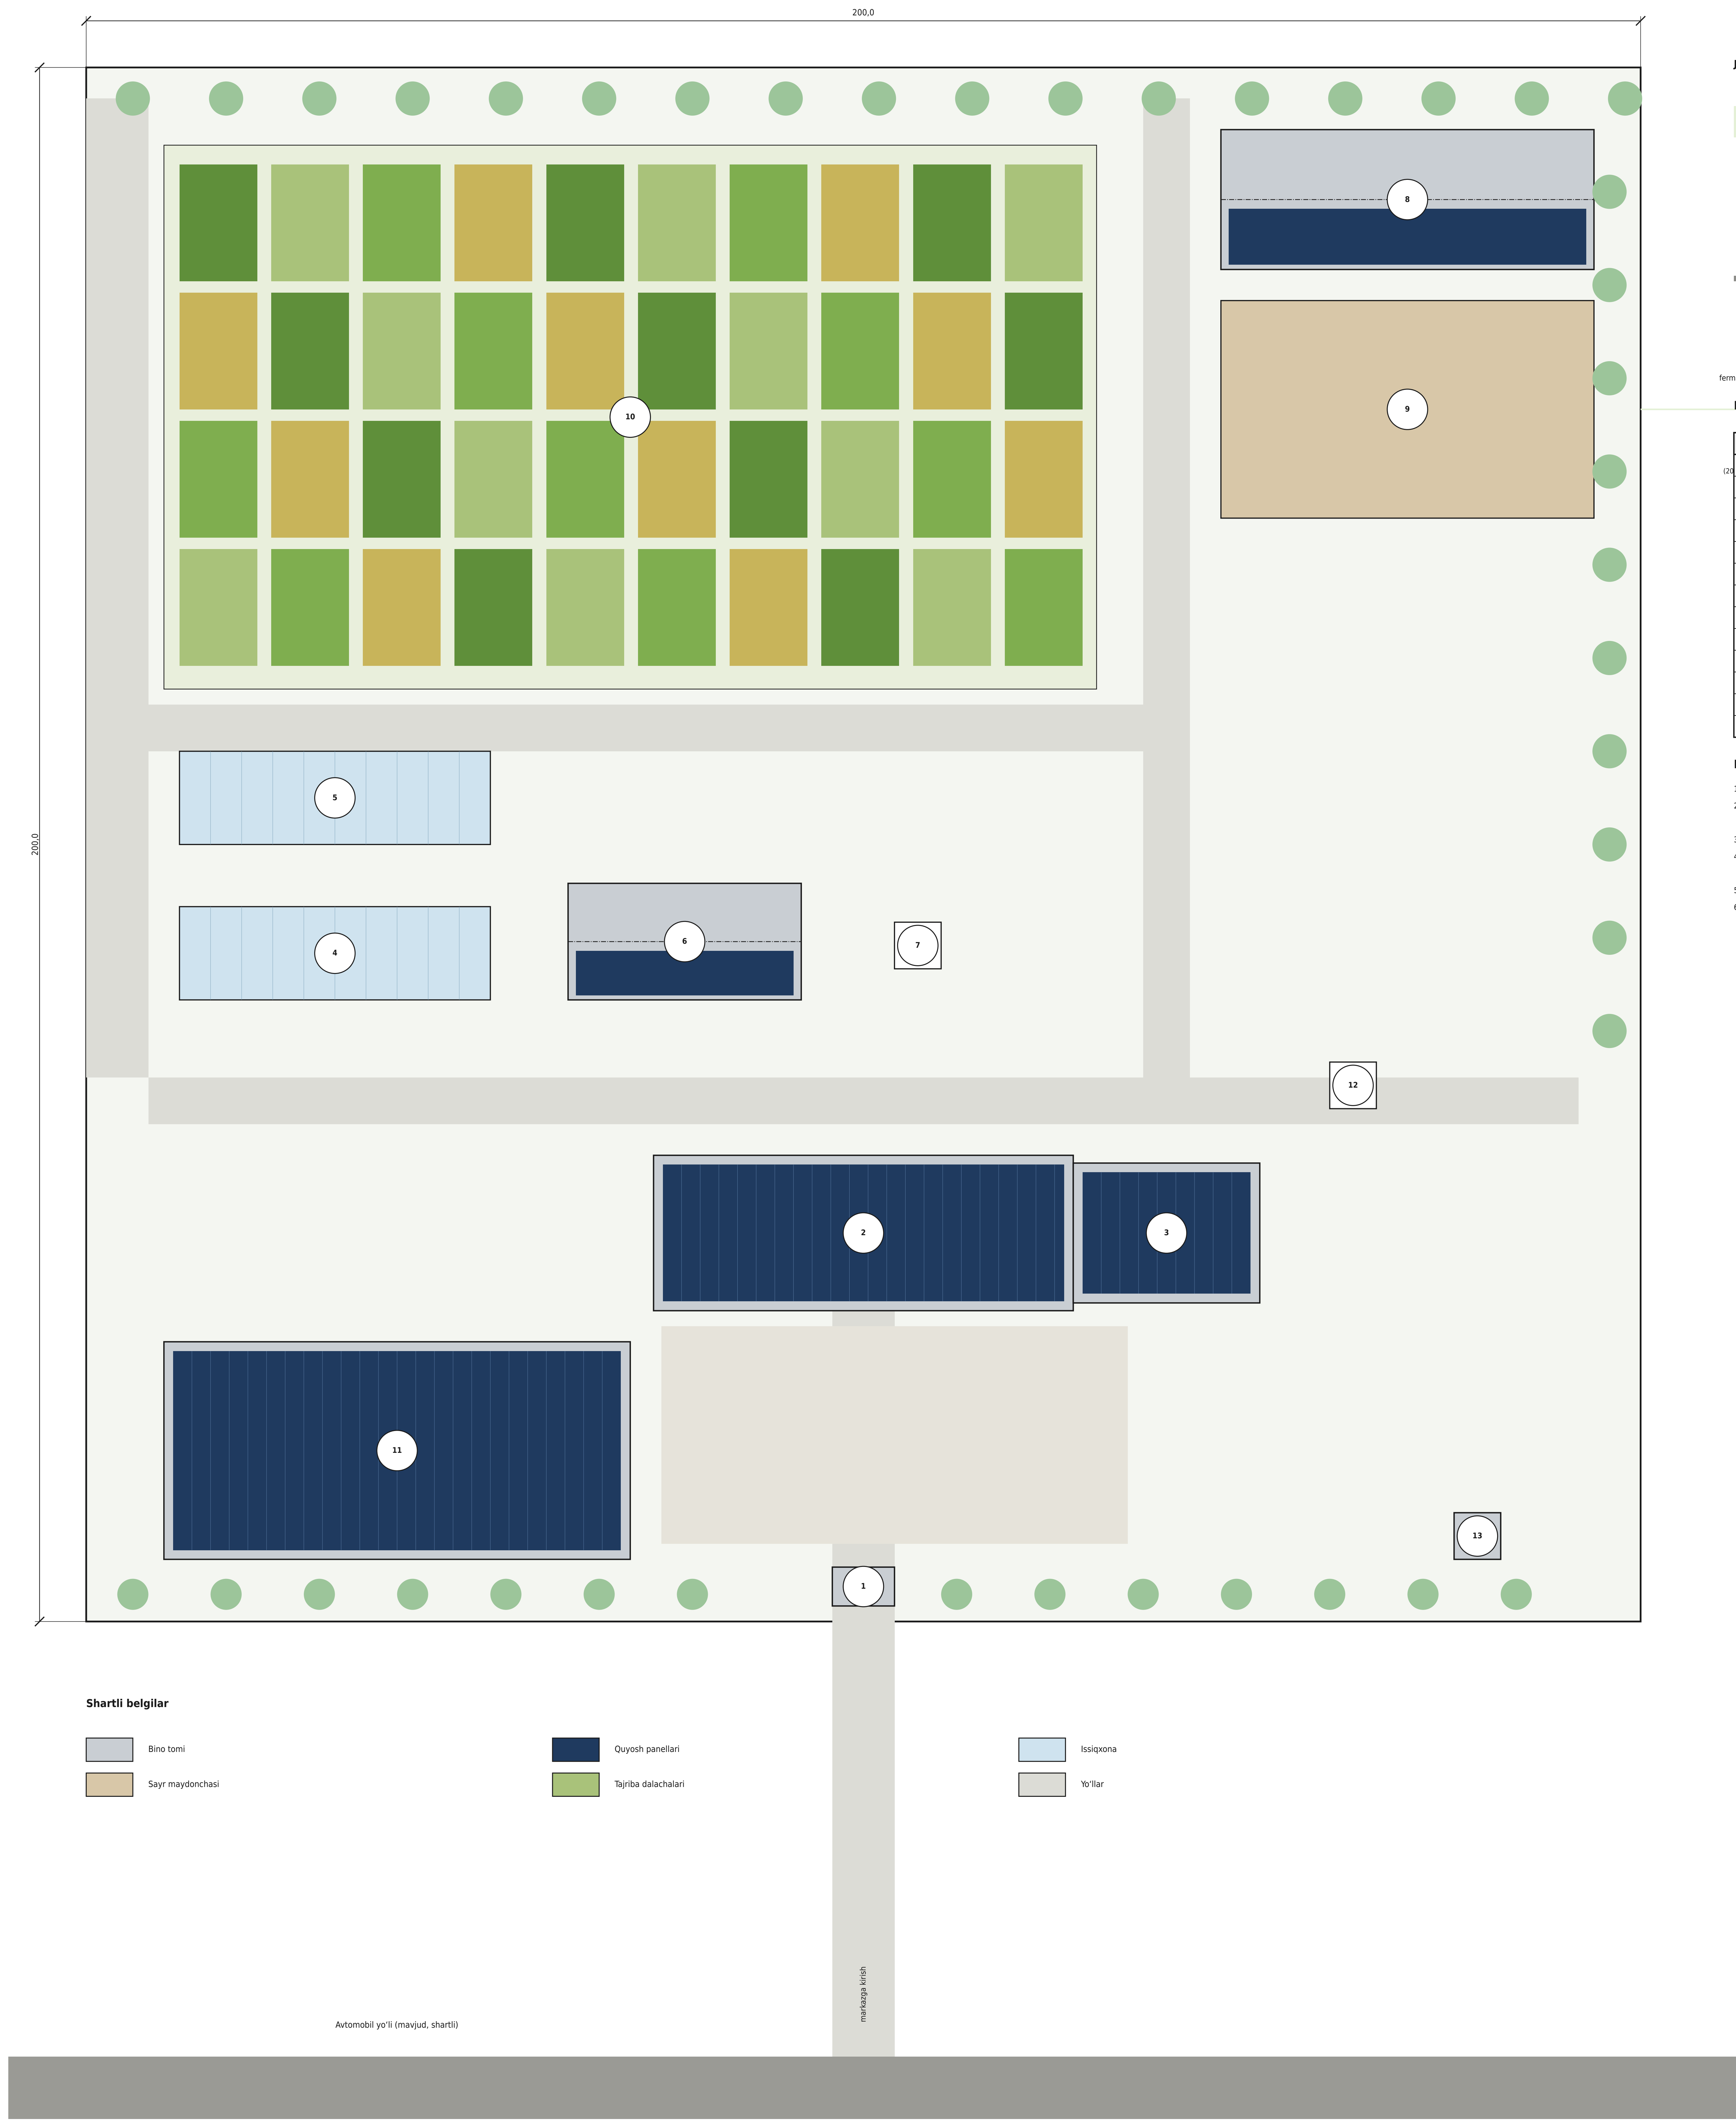

Joylashuv sxemasi · M 1:10000

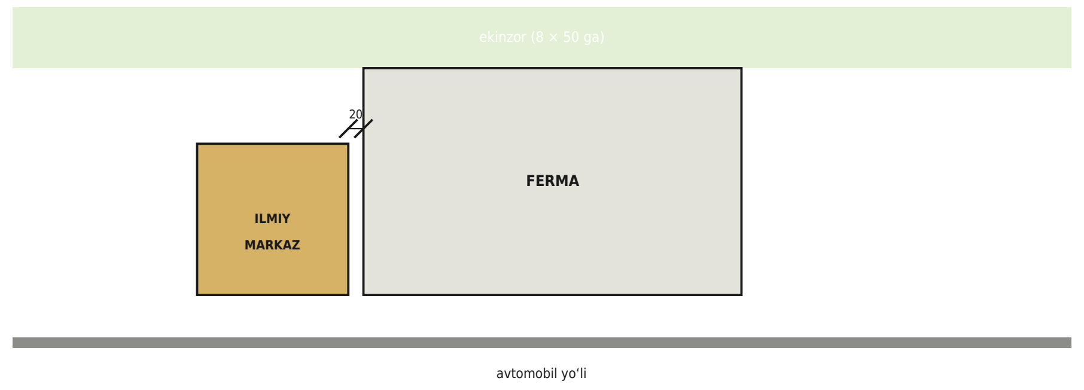

Binolar va inshootlar eksplikatsiyasi

№	Nomi	O‘lcham, m	Maydon, m²
1	Nazorat-o‘tkazish punkti	8 × 5	40
2	Ilmiy-laboratoriya minorasi (5 qavat)	54 × 20	5 400
3	O‘quv-konferensiya zali (120 o‘rin)	24 × 18	432
4	Issiqxona-1: seleksiya	40 × 12	480
5	Issiqxona-2: urug‘chilik	40 × 12	480
6	Urug‘ ombori va agrotexnika ayvoni	30 × 15	450
7	Meteostansiya	6 × 6	36
8	Tajriba molxonasi (40 bosh)	48 × 18	864
9	Tajriba molxonasi sayr maydonchasi	48 × 28	1 344
10	Tajriba dalachalari (40 ta, 10 × 15 m)	120 × 70	8 400
11	Avtoturargoh, quyosh soyaboni (70 joy)	60 × 28	1 680
12	Suyuq azot rezervuari	6 × 6	36
13	Transformator punkti	6 × 6	36

Tadqiqot yo‘nalishlari

Naslchilik:
  genomik baholash va naslni tanlash (DNK chiplar);
  sun’iy urug‘lantirish, embrion ko‘chirib o‘tkazish;
  urug‘ va embrionlar kriobanki;
  sut va ozuqa sifati, oziqlantirish tajribalari
  (40 boshlik tajriba molxonasi);
  veterinariya diagnostikasi.
Dehqonchilik:
  tuproq va agrokimyo tahlili;
  seleksiya va urug‘chilik (2 issiqxona, 40 dalacha);
  sug‘orish tajribalari (tomchilatib va yomg‘irlatib);
  meteostansiya, dron va sun’iy yo‘ldosh monitoringi.
Joriy etish: fermerlar uchun o‘quv-konferensiya
  zali, natijalarni ekinzor va fermada sinash.

Eslatmalar

1. Markaz fermaning yonida, janubi-g‘arbiy darvoza tomonida; fermadan 20 m, o‘z kirish yo‘li bilan.
2. Tajriba molxonasi uchastkaning shimoli-sharqiy chekka burchagida, minoradan ≈ 115 m uzoqda; hayvonlar fermaga sharqiy to‘siqdagi alohida yo‘lak orqali o‘tadi, laboratoriya zonasi bilan kesishmaydi.
3. Quyosh panellari faqat tomlarda va avtoturargoh soyabonida; yerga panel o‘rnatilmaydi.
4. Xodimlar 100: ma’muriyat 10, naslchilik 22, dehqonchilik 18, laborantlar 24, IT va bioinformatika 8, o‘quv markazi va joriy etish 8, molxona, issiqxona va dalachalar ishchilari 10.
5. DNK genotiplash tashqi laboratoriyada (50K test 39–41 $); skaner sotib olinmaydi.
6. Tomlarda ≈ 0,54 MWp quyosh paneli, yiliga ≈ 0,76 GWh — markaz iste’molining ≈ 85%.

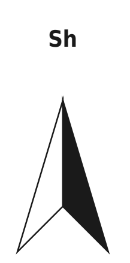

Investitsiya hisobi (taxmin, mln $)

Modda	mln $
Ilmiy minora 5 400 m² × 750 $	4,05
O‘quv zali 432 m² × 600 $	0,26
Laboratoriya jihozlari (genotiplash tashqarida)	1,40
Issiqxonalar 960 m² × 250 $	0,24
Tajriba molxonasi va 20 ta oziqlantirish stansiyasi	0,43
Urug‘ ombori, dalachalar, meteo, dron	0,26
Quyosh panellari ≈ 0,54 MWp	0,41
Tarmoqlar, yo‘llar, to‘siq, obodonlashtirish	0,35
Loyihalash va kutilmagan xarajatlar (8%)	0,59
Jami	**7,99**

Yillik ishlash xarajati ≈ 1,4 mln $: ish haqi ≈ 1,06,
reaktivlar, DNK testlari, suyuq azot, ta’mirlash ≈ 0,35.
12-varaqqa hali kiritilmagan.

Almashtirilgan inv. №
Imzo va sana
Asl nusxa inv. №

O‘zg.	Varaq	Hujjat №	Imzo	Sana
Ishlab chiqdi				10.2026
Tekshirdi				10.2026
Bosh muhandis				10.2026
Normativ nazorat				10.2026
Tasdiqladi				10.2026

MS-2026-TEO

Meat Solutions — integratsiyalashgan go‘sht klasteri

Ilmiy-innovatsion markaz bosh rejasi (4,0 ga)

Masshtab: 1:500, 1:10000

Bosqich	Varaq	Varaqlar
TEO oldi	20	21

Meat Solutions
Toshkent viloyati, 2026