
NASLLI FERMA — BOSH REJA

15,0 ga · 500 × 300 m · Simmental zoti: 400 sigir, 600 g‘unajin, 160 buzoq, 240 bo‘rdoqi · biogaz va quyosh panellari

MEAT SOLUTIONS

Toshkent viloyati · 2026 · MS-2026-TEO

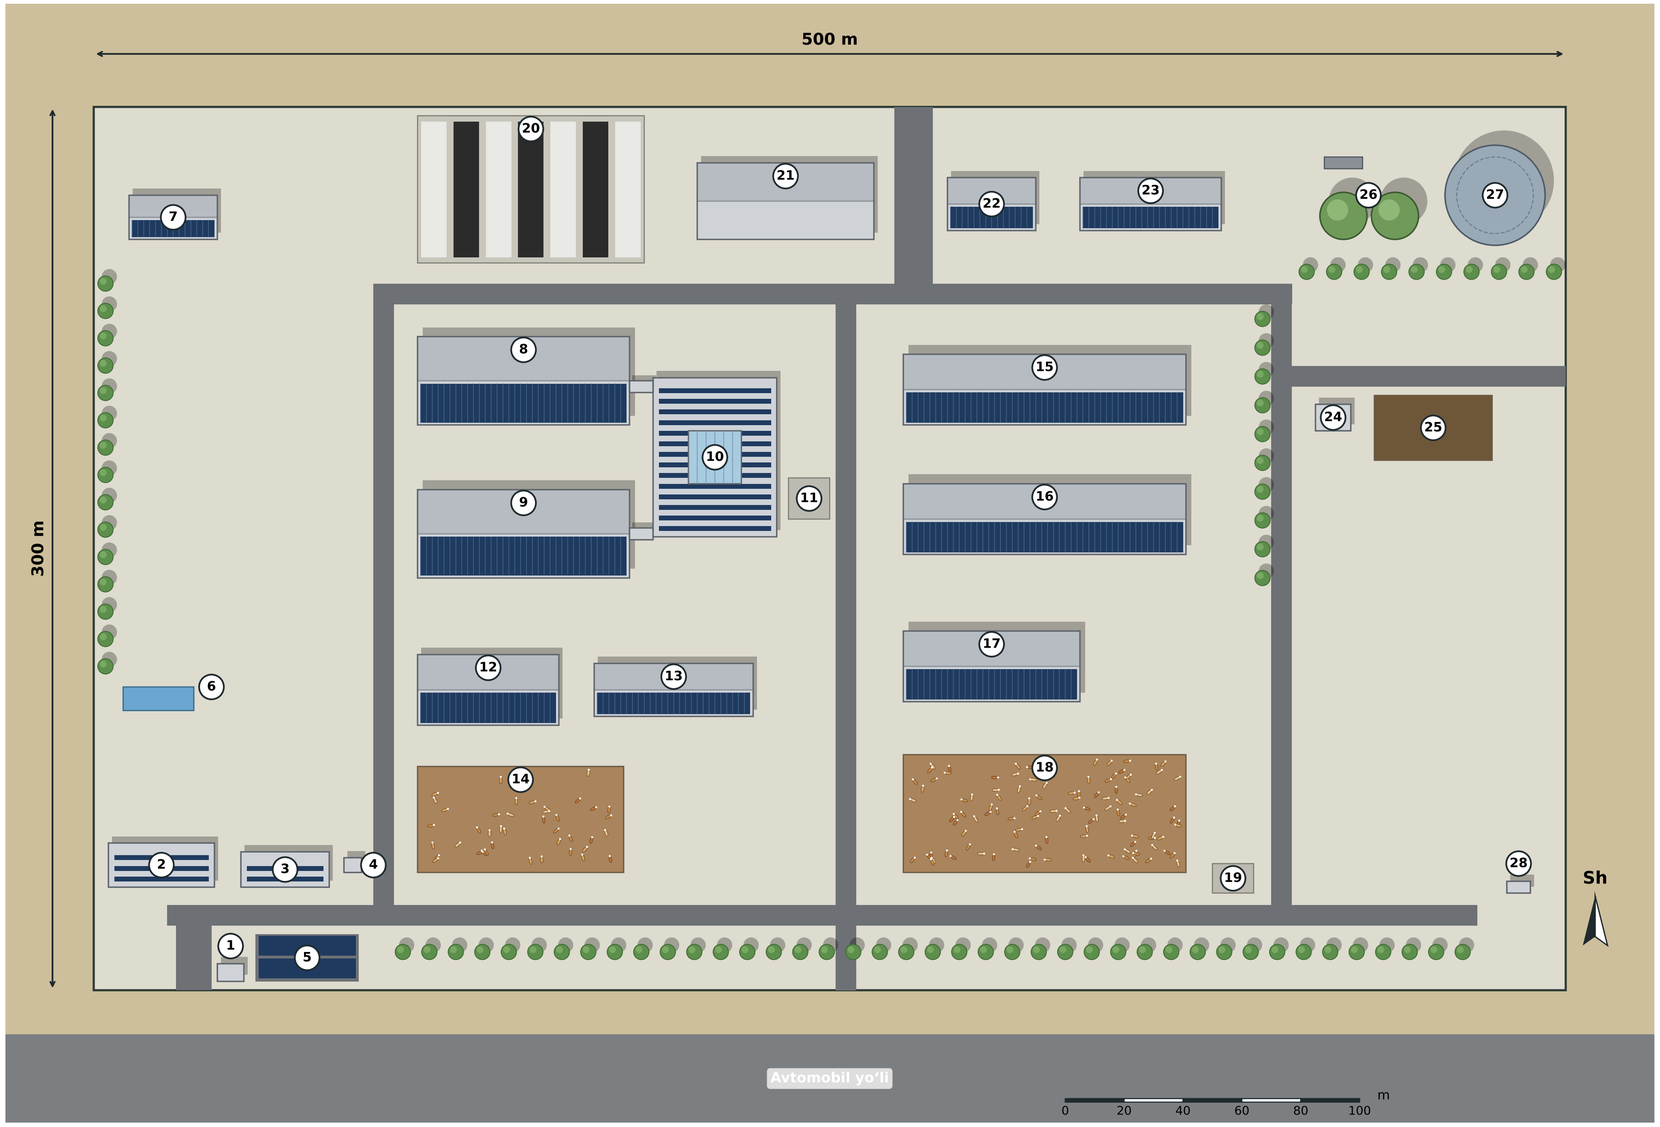

Binolar va inshootlar

№	Nomi	O‘lchami, m	Maydoni, m²
1	Nazorat-o‘tkazish punkti	9 × 6	54
2	Ma’muriy-maishiy bino (sanitariya o‘tkazgichi bilan)	36 × 15	540
3	Veterinariya bloki va sun’iy urug‘lantirish punkti	30 × 12	360
4	Transformator podstansiyasi 10/0,4 kV	6 × 5	30
5	Avtoturargoh (40 joy)	35 × 16	560
6	Yong‘inga qarshi suv havzalari (2 × 100 m³)	24 × 8	192
7	Karantin va izolyator (alohida to‘siq bilan)	30 × 15	450
8	Sigirxona-1 (200 boks, 180 sigir)	72 × 30	2 160
9	Sigirxona-2 (200 boks, 180 sigir)	72 × 30	2 160
10	Sog‘ish zali (karusel, 40 joy) va sut bloki	42 × 54	2 268
11	Sut mashinasi maydonchasi	14 × 14	196
12	Tug‘ruqxona va quruq sigirlar binosi (60 joy)	48 × 24	1 152
13	Buzoqxona (160 joy)	54 × 18	972
14	Sayr maydonchasi (quruq sigirlar)	70 × 36	2 520
15	G‘unajinxona-1 (300 joy)	96 × 24	2 304
16	G‘unajinxona-2 (300 joy)	96 × 24	2 304
17	Bo‘rdoqi bloki (240 joy)	60 × 24	1 440
18	G‘unajinlar sayr maydonchasi	96 × 40	3 840
19	Chorva yuklash rampasi va tarozi	14 × 10	140
20	Silos-senaj transheyalari (7 × 11 × 50 m)	77 × 50	3 850
21	Pichan ombori (shiypon)	60 × 26	1 560
22	Don ombori va kombikorm sexi	30 × 18	540
23	Texnika parki va ustaxona	48 × 18	864
24	Go‘ng separatori binosi	12 × 9	108
25	Qattiq go‘ng maydonchasi (beton, devorli)	40 × 22	880
26	Biogaz reaktorlari 2 × 1 800 m³ va kogeneratsiya (…	36 × 40	1 440
27	Digestat ombori, yopiq (≈ 5 000 m³)	36 × 40	1 440
28	O‘lgan hayvonlarni vaqtincha saqlash (sovutgichli …	8 × 4	32

Asosiy ko‘rsatkichlar

Uchastka	**500 × 300 m = 15,0 ga**
Binolar egallagan maydon	**24 168 m² (16%)**
Sigirxonalar	**2 × 200 boks**
Sog‘ish	**tashqi karusel, 40 joy, 240–300 sigir/soat**
Quyosh panellari	**1,67 MWp, 2,39 GWh/yil**
Biogaz	**≈ 250 kWe, ≈ 2,0 GWh/yil**
Robotlar	**2 ozuqa itaruvchi, 4 go‘ng tozalovchi**
Ish o‘rinlari	**≈ 85**