
QUSHXONA VA MUZLATGICH — BOSH REJA

12,56 ga · 400 × 314 m · smenada 100 bosh qoramol va 300 bosh qo‘y-echki · muzlatgich 3 000 t

MEAT SOLUTIONS

Toshkent viloyati · 2026 · MS-2026-TEO

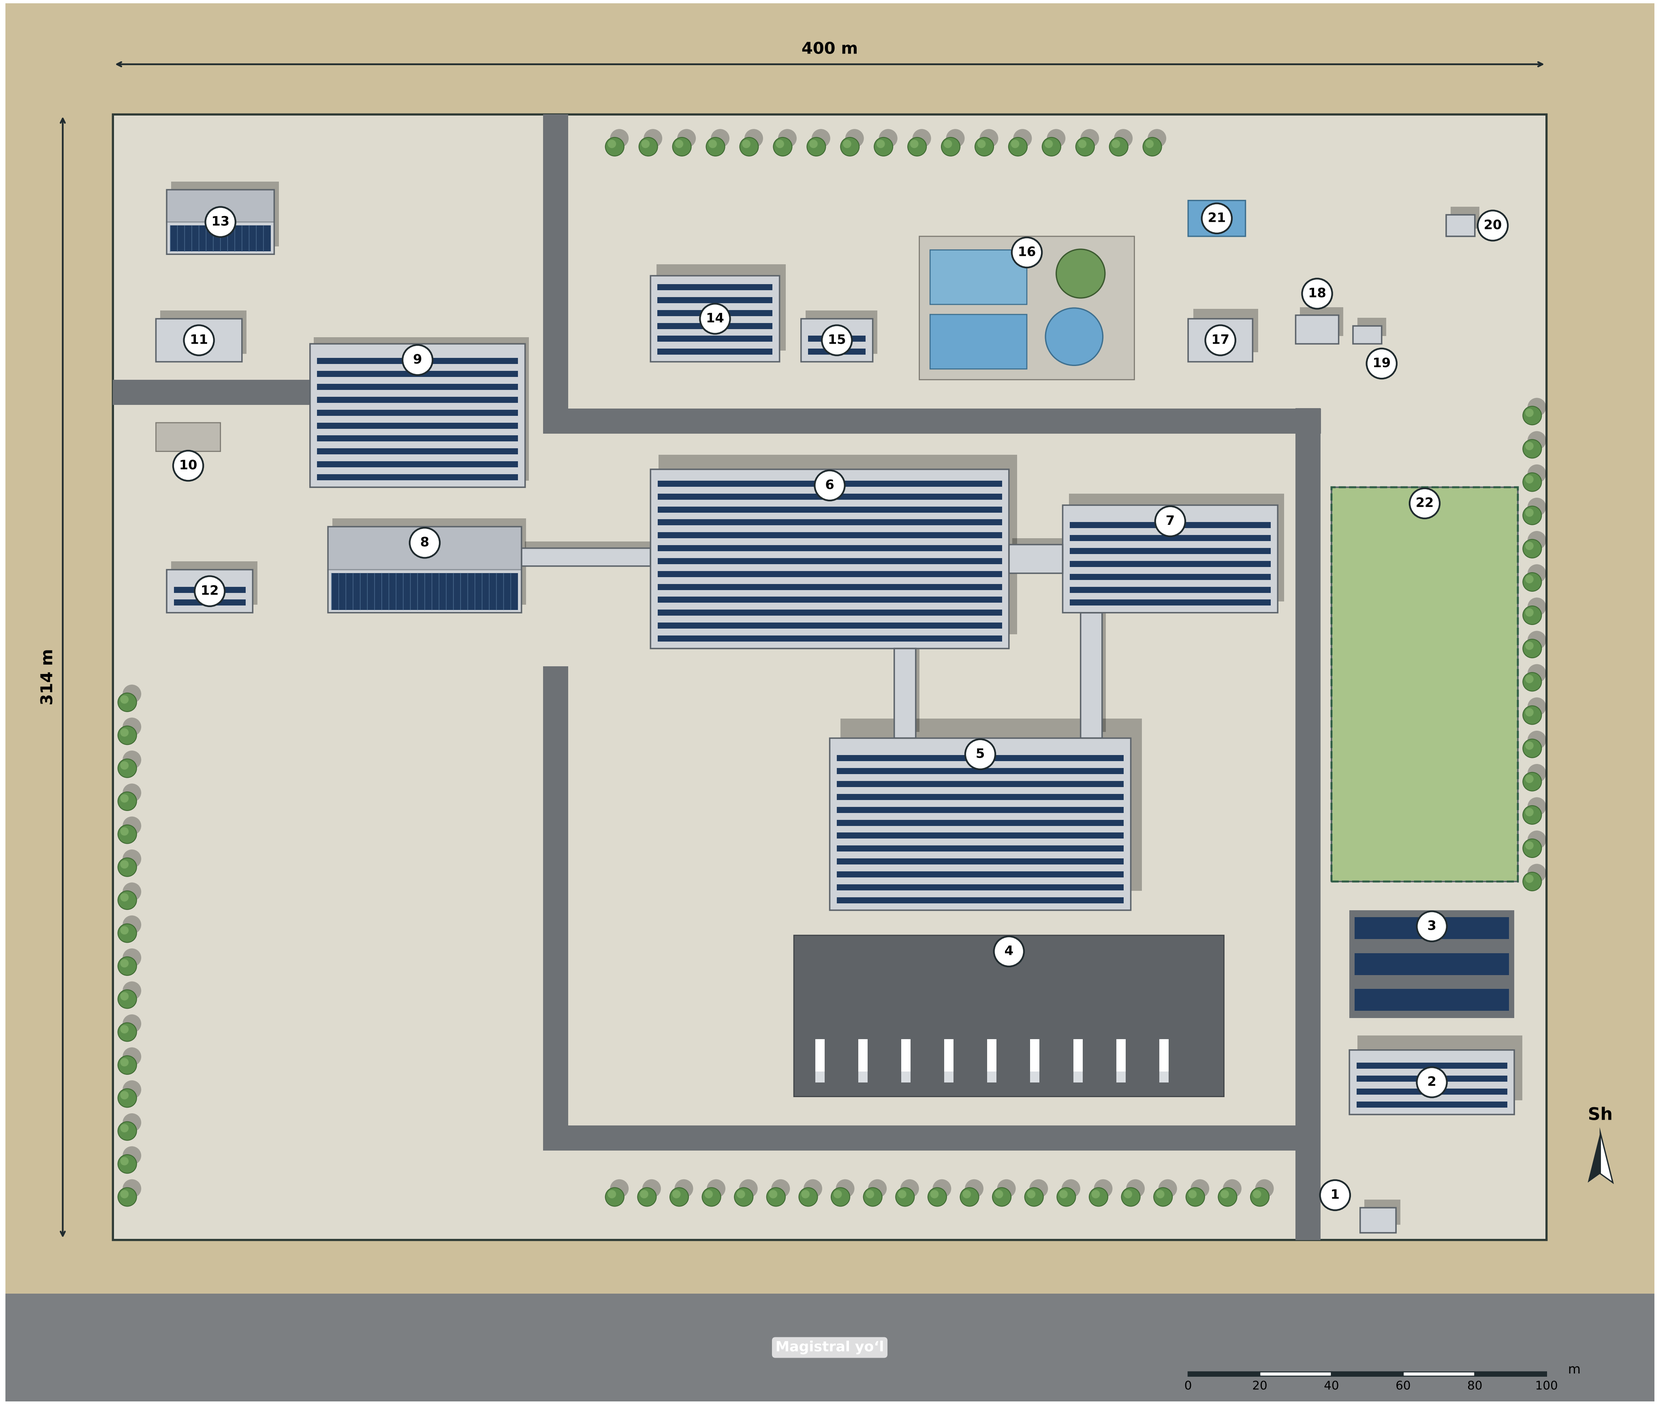

Binolar va inshootlar

№	Nomi	O‘lchami, m	Maydoni, m²
1	Nazorat-o‘tkazish punkti (asosiy)	10 × 7	70
2	Ma’muriy bino (2 qavat)	46 × 18	828
3	Avtoturargoh (60 joy)	46 × 30	1 380
4	Ekspeditsiya maydonchasi (yuk mashinalari)	120 × 45	5 400
5	Muzlatgich 3 000 t, avtomat yuqori stellajli ombor…	84 × 48	4 032
6	Qushxona binosi (so‘yish va tusha sovutish)	100 × 50	5 000
7	Qayta ishlash sexi	60 × 30	1 800
8	So‘yish oldi chorva saqlash binosi	54 × 24	1 296
9	Ochiq qo‘ralar (navesli)	60 × 40	2 400
10	Chorva tushirish rampasi va qabul joyi	18 × 8	144
11	Transport yuvish va dezinfeksiya punkti	24 × 12	288
12	Veterinariya laboratoriyasi va chorva qabul ofisi	24 × 12	288
13	Karantin, izolyator va sanitariya so‘yish xonasi	30 × 18	540
14	Qo‘shimcha mahsulot sexi (yog‘ eritish, suyak-go‘s…	36 × 24	864
15	Teri va texnik chiqindilar ombori	20 × 12	240
16	Oqova suv tozalash inshooti va biogaz reaktori (≈ …	60 × 40	2 400
17	Bug‘ qozonxonasi	18 × 12	216
18	Bosh transformator podstansiyasi 10/0,4 kV	12 × 8	96
19	Rezerv dizel-generator	8 × 5	40
20	Nasos stansiyasi (suv ta’minoti)	8 × 6	48
21	Yong‘inga qarshi suv havzasi	16 × 10	160
22	2-bosqich uchun zaxira (muzlatgich kengaytmasi, ko…	52 × 110	5 720

Asosiy ko‘rsatkichlar

Uchastka	**400 × 314 m = 12,56 ga**
Binolar egallagan maydon	**18 190 m² (14%)**
Go‘sht	**≈ 7 775 t/yil**
Muzlatgich	**3 000 t, shok 40 t/sutka, 8 dok**
Quyosh panellari	**2,33 MWp, 3,23 GWh/yil**
Oqova suv	**≈ 250 m³/sutka, biogaz bilan**
Elektr	**10/0,4 kV podstansiya, dizel-generator**
Ish o‘rinlari	**≈ 320**